





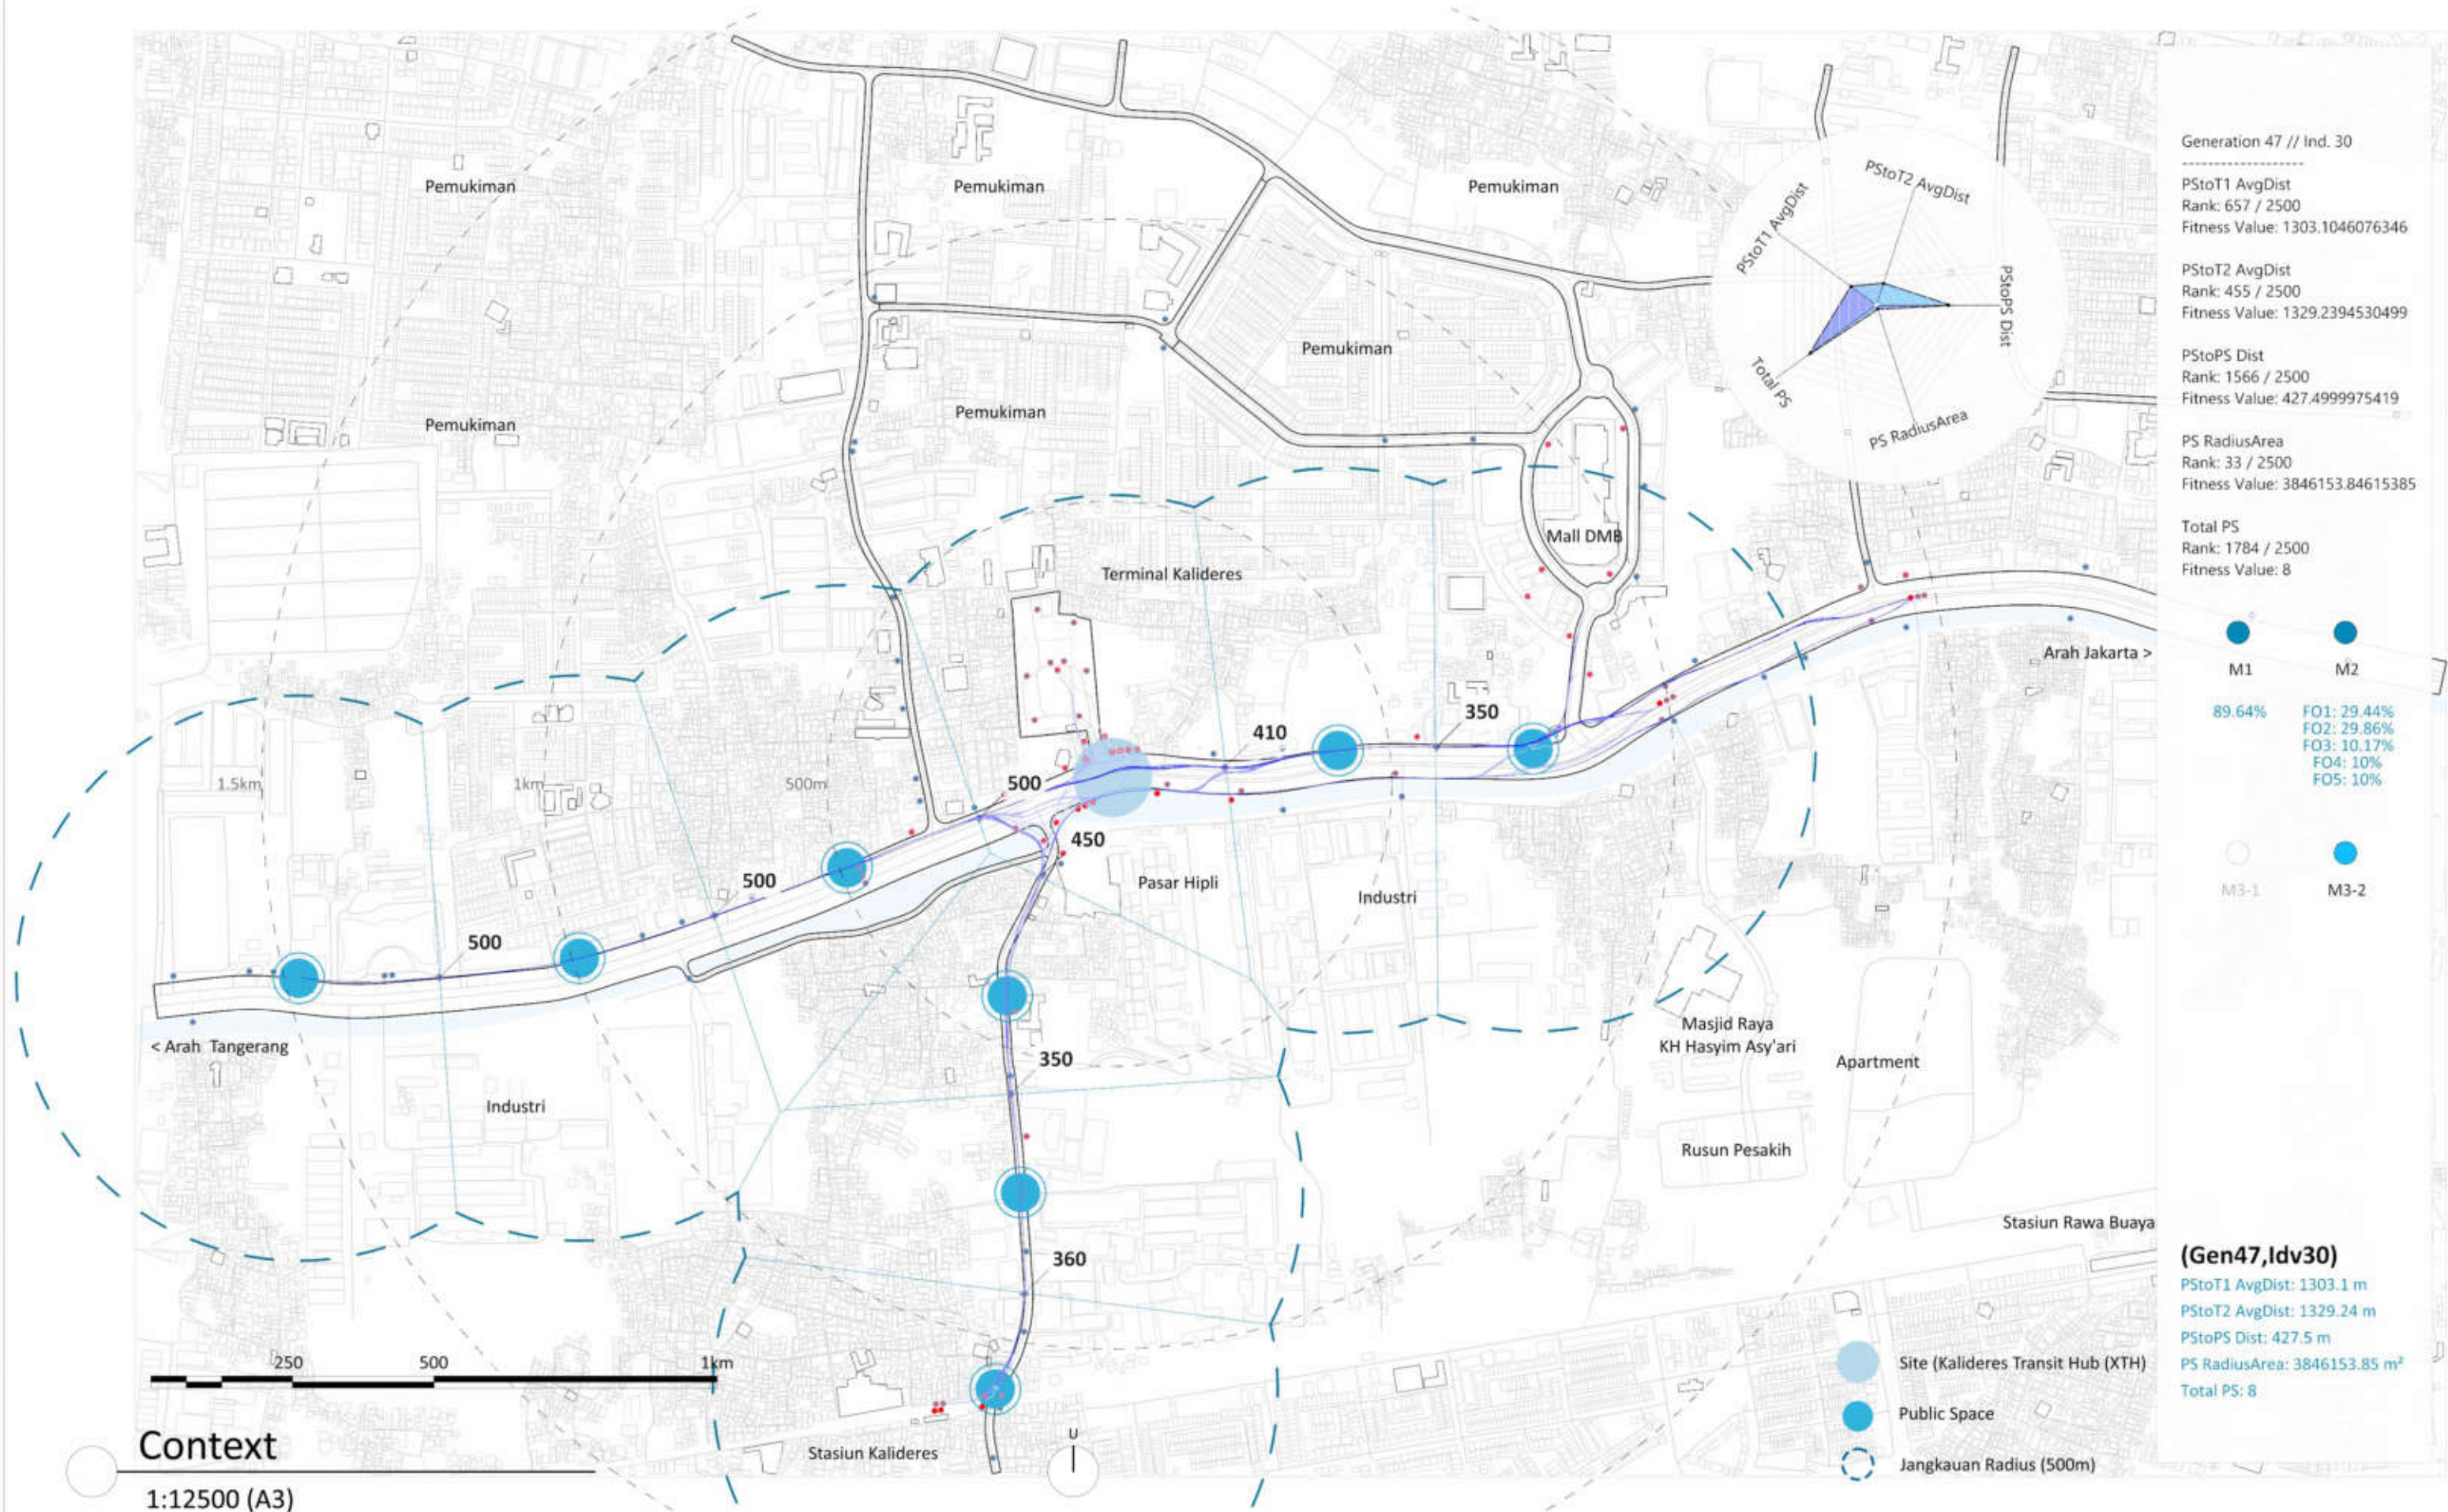

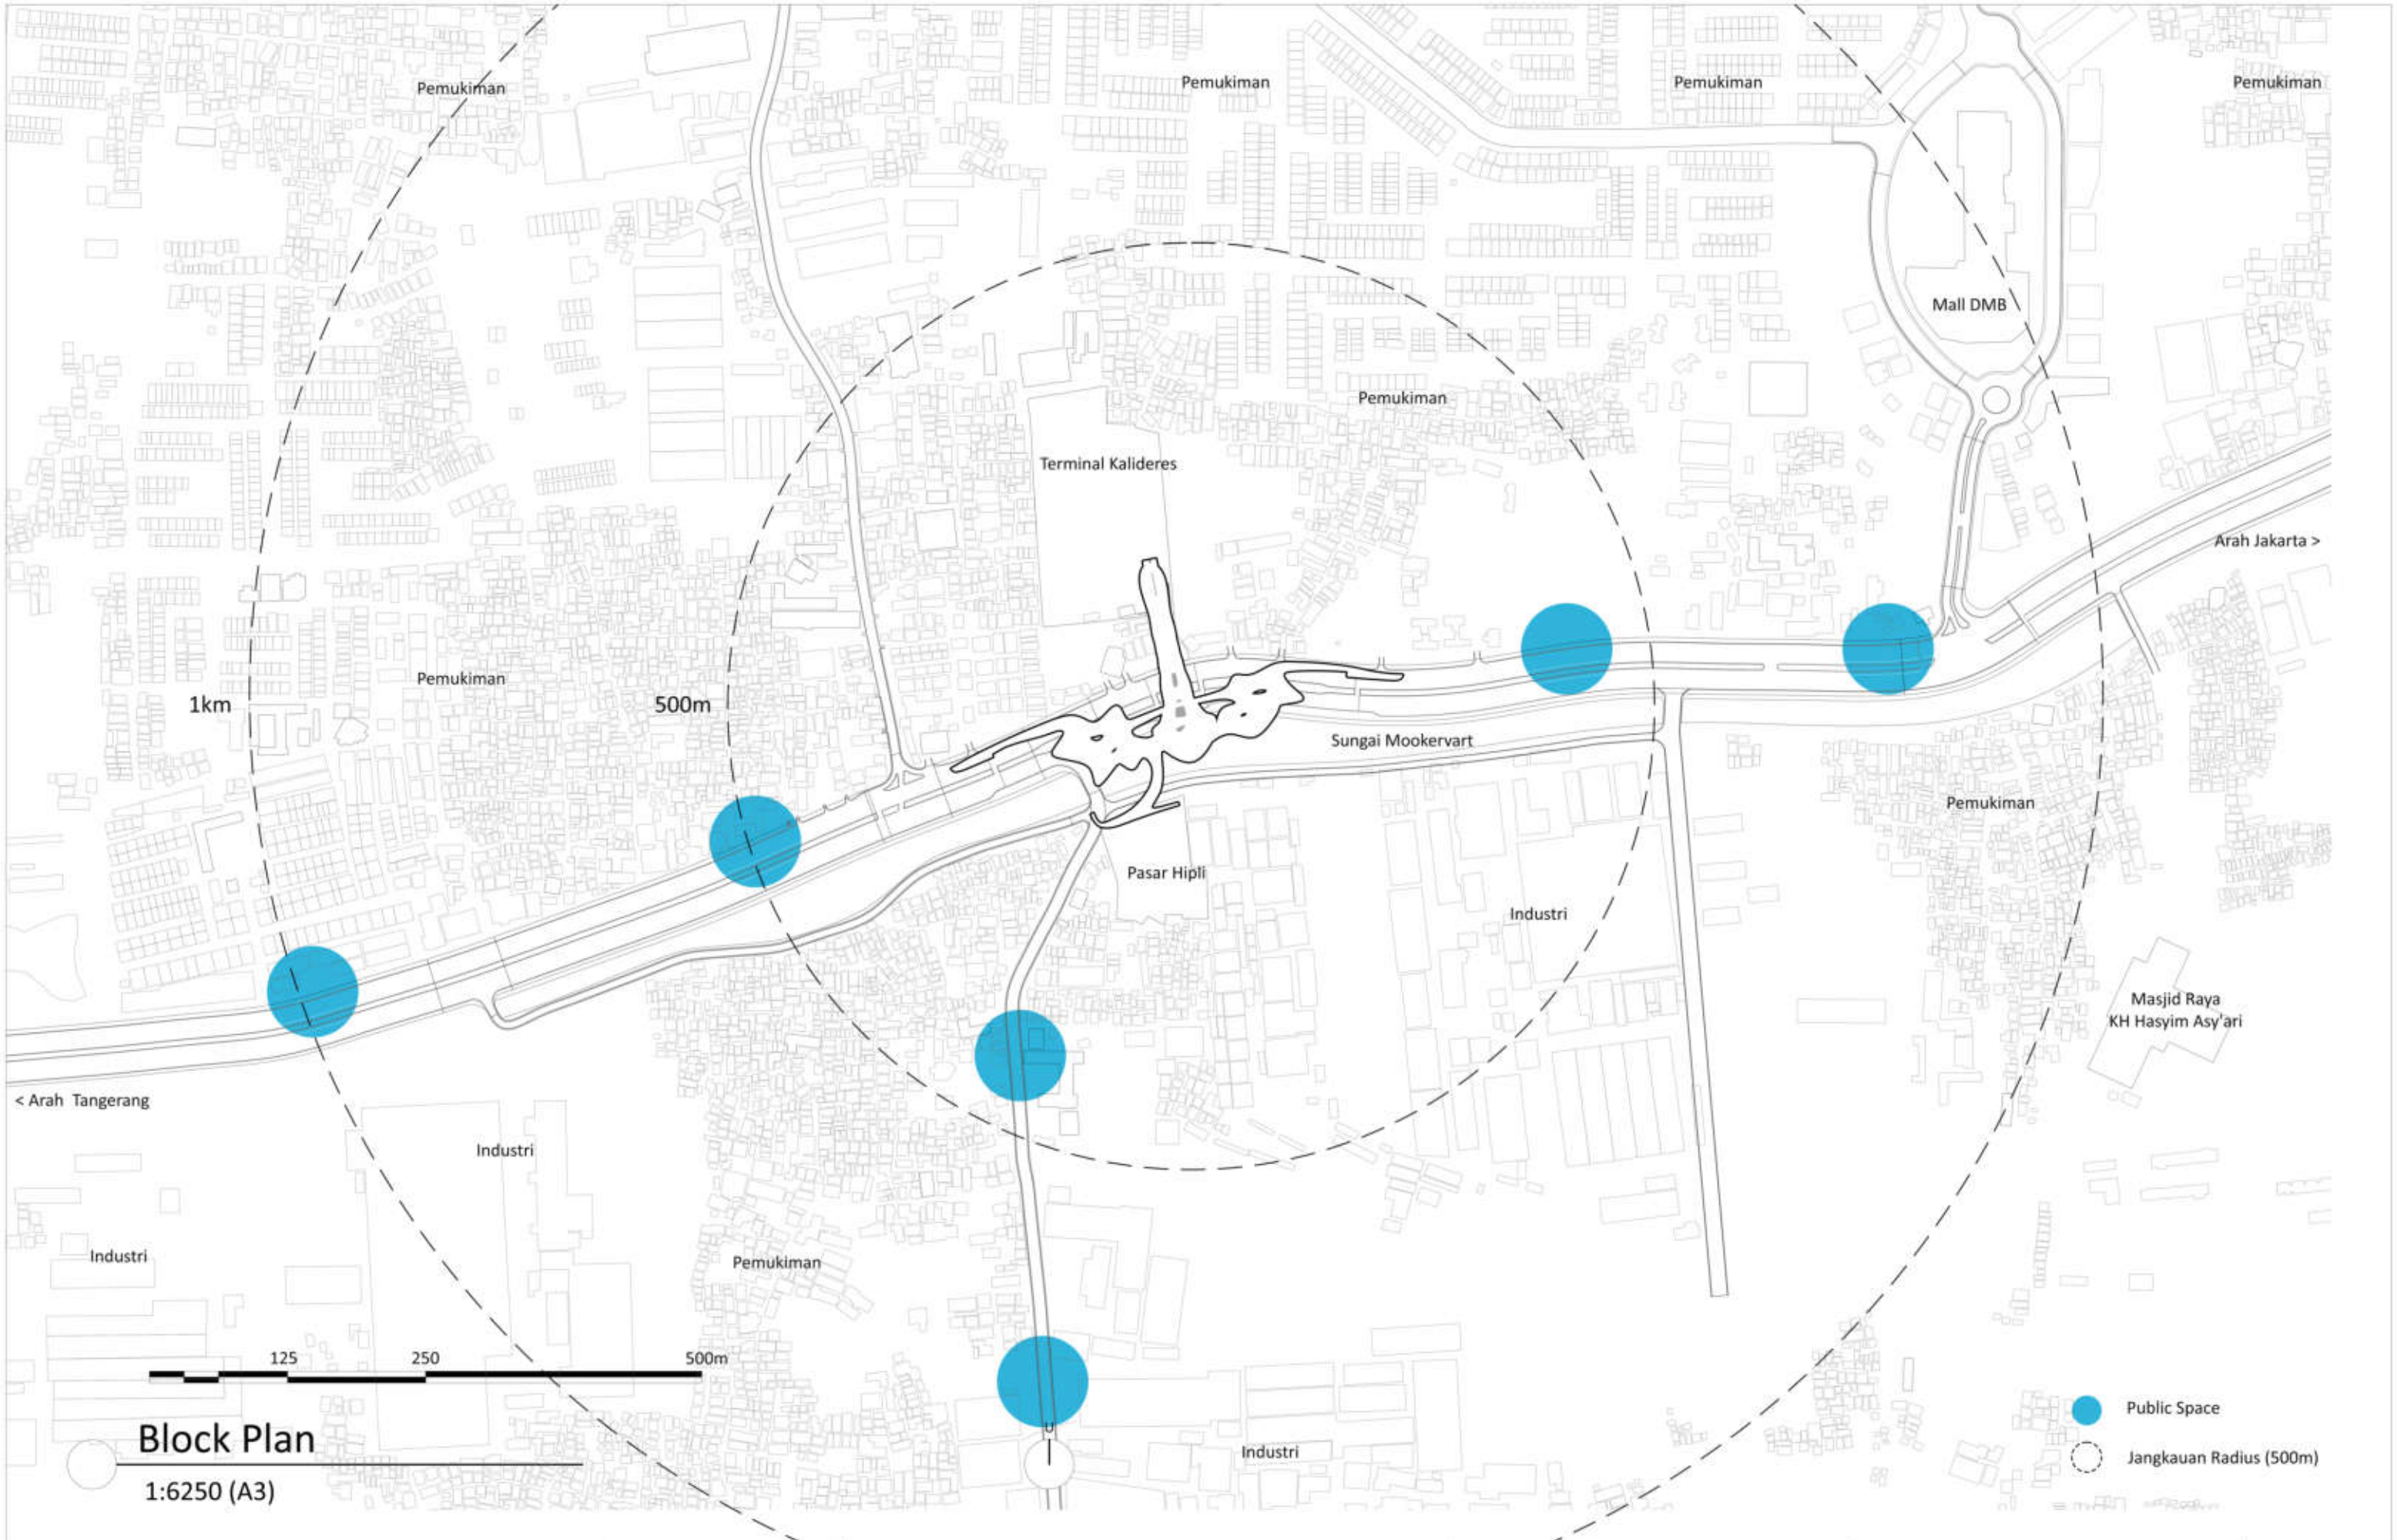


 Program Studi Magister Arsitektur Sekolah Arsitektur, Perencanaan, dan Pengembangan Kebijakan Institut Teknologi Bandung	AR6690 Tesis Semester 1 2022/2023	Kalideres Transit Hub (XTH)	Dosen Pembimbing: Aswin Indraprastha, S.T., M.T., M.Eng., Ph.D. Dosen Koordinator: Dewi Larasati, S.T, M.T, Ph.D.	Nama Mahasiswa: Arnett Ferels NIM: 25221029	Tanggal: 25/01/2023
--	--	------------------------------------	---	---	--------------------------------

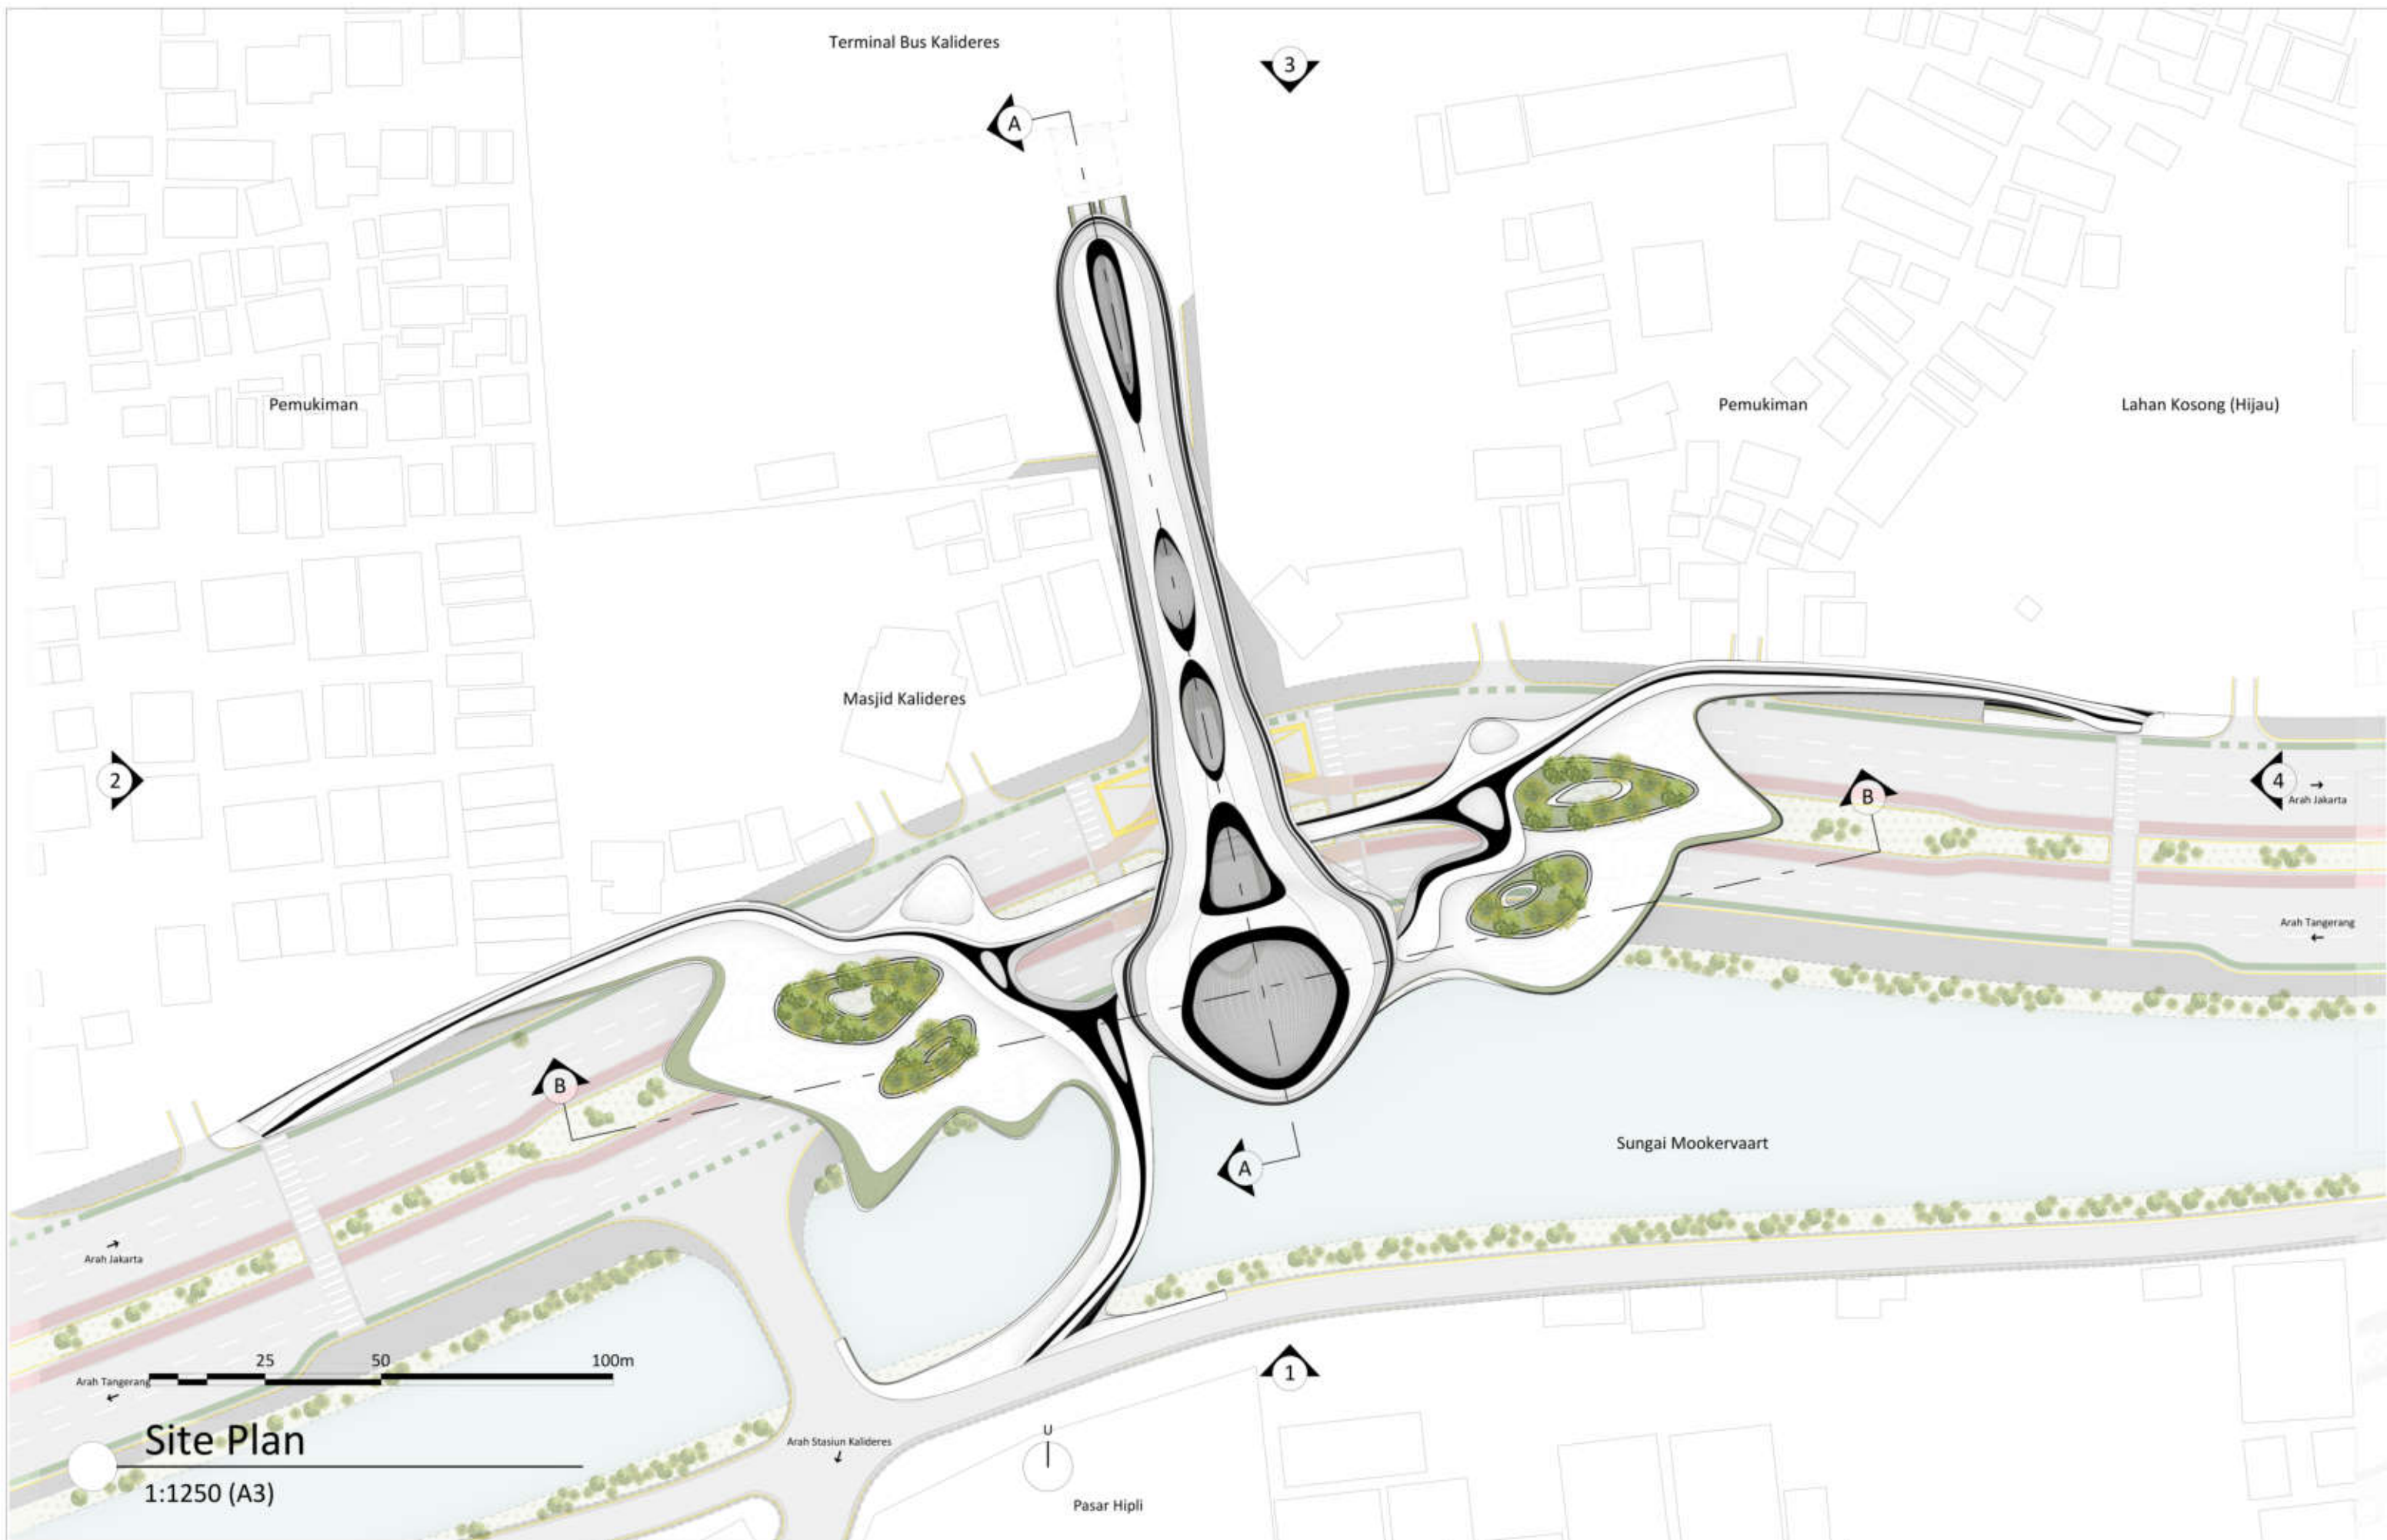

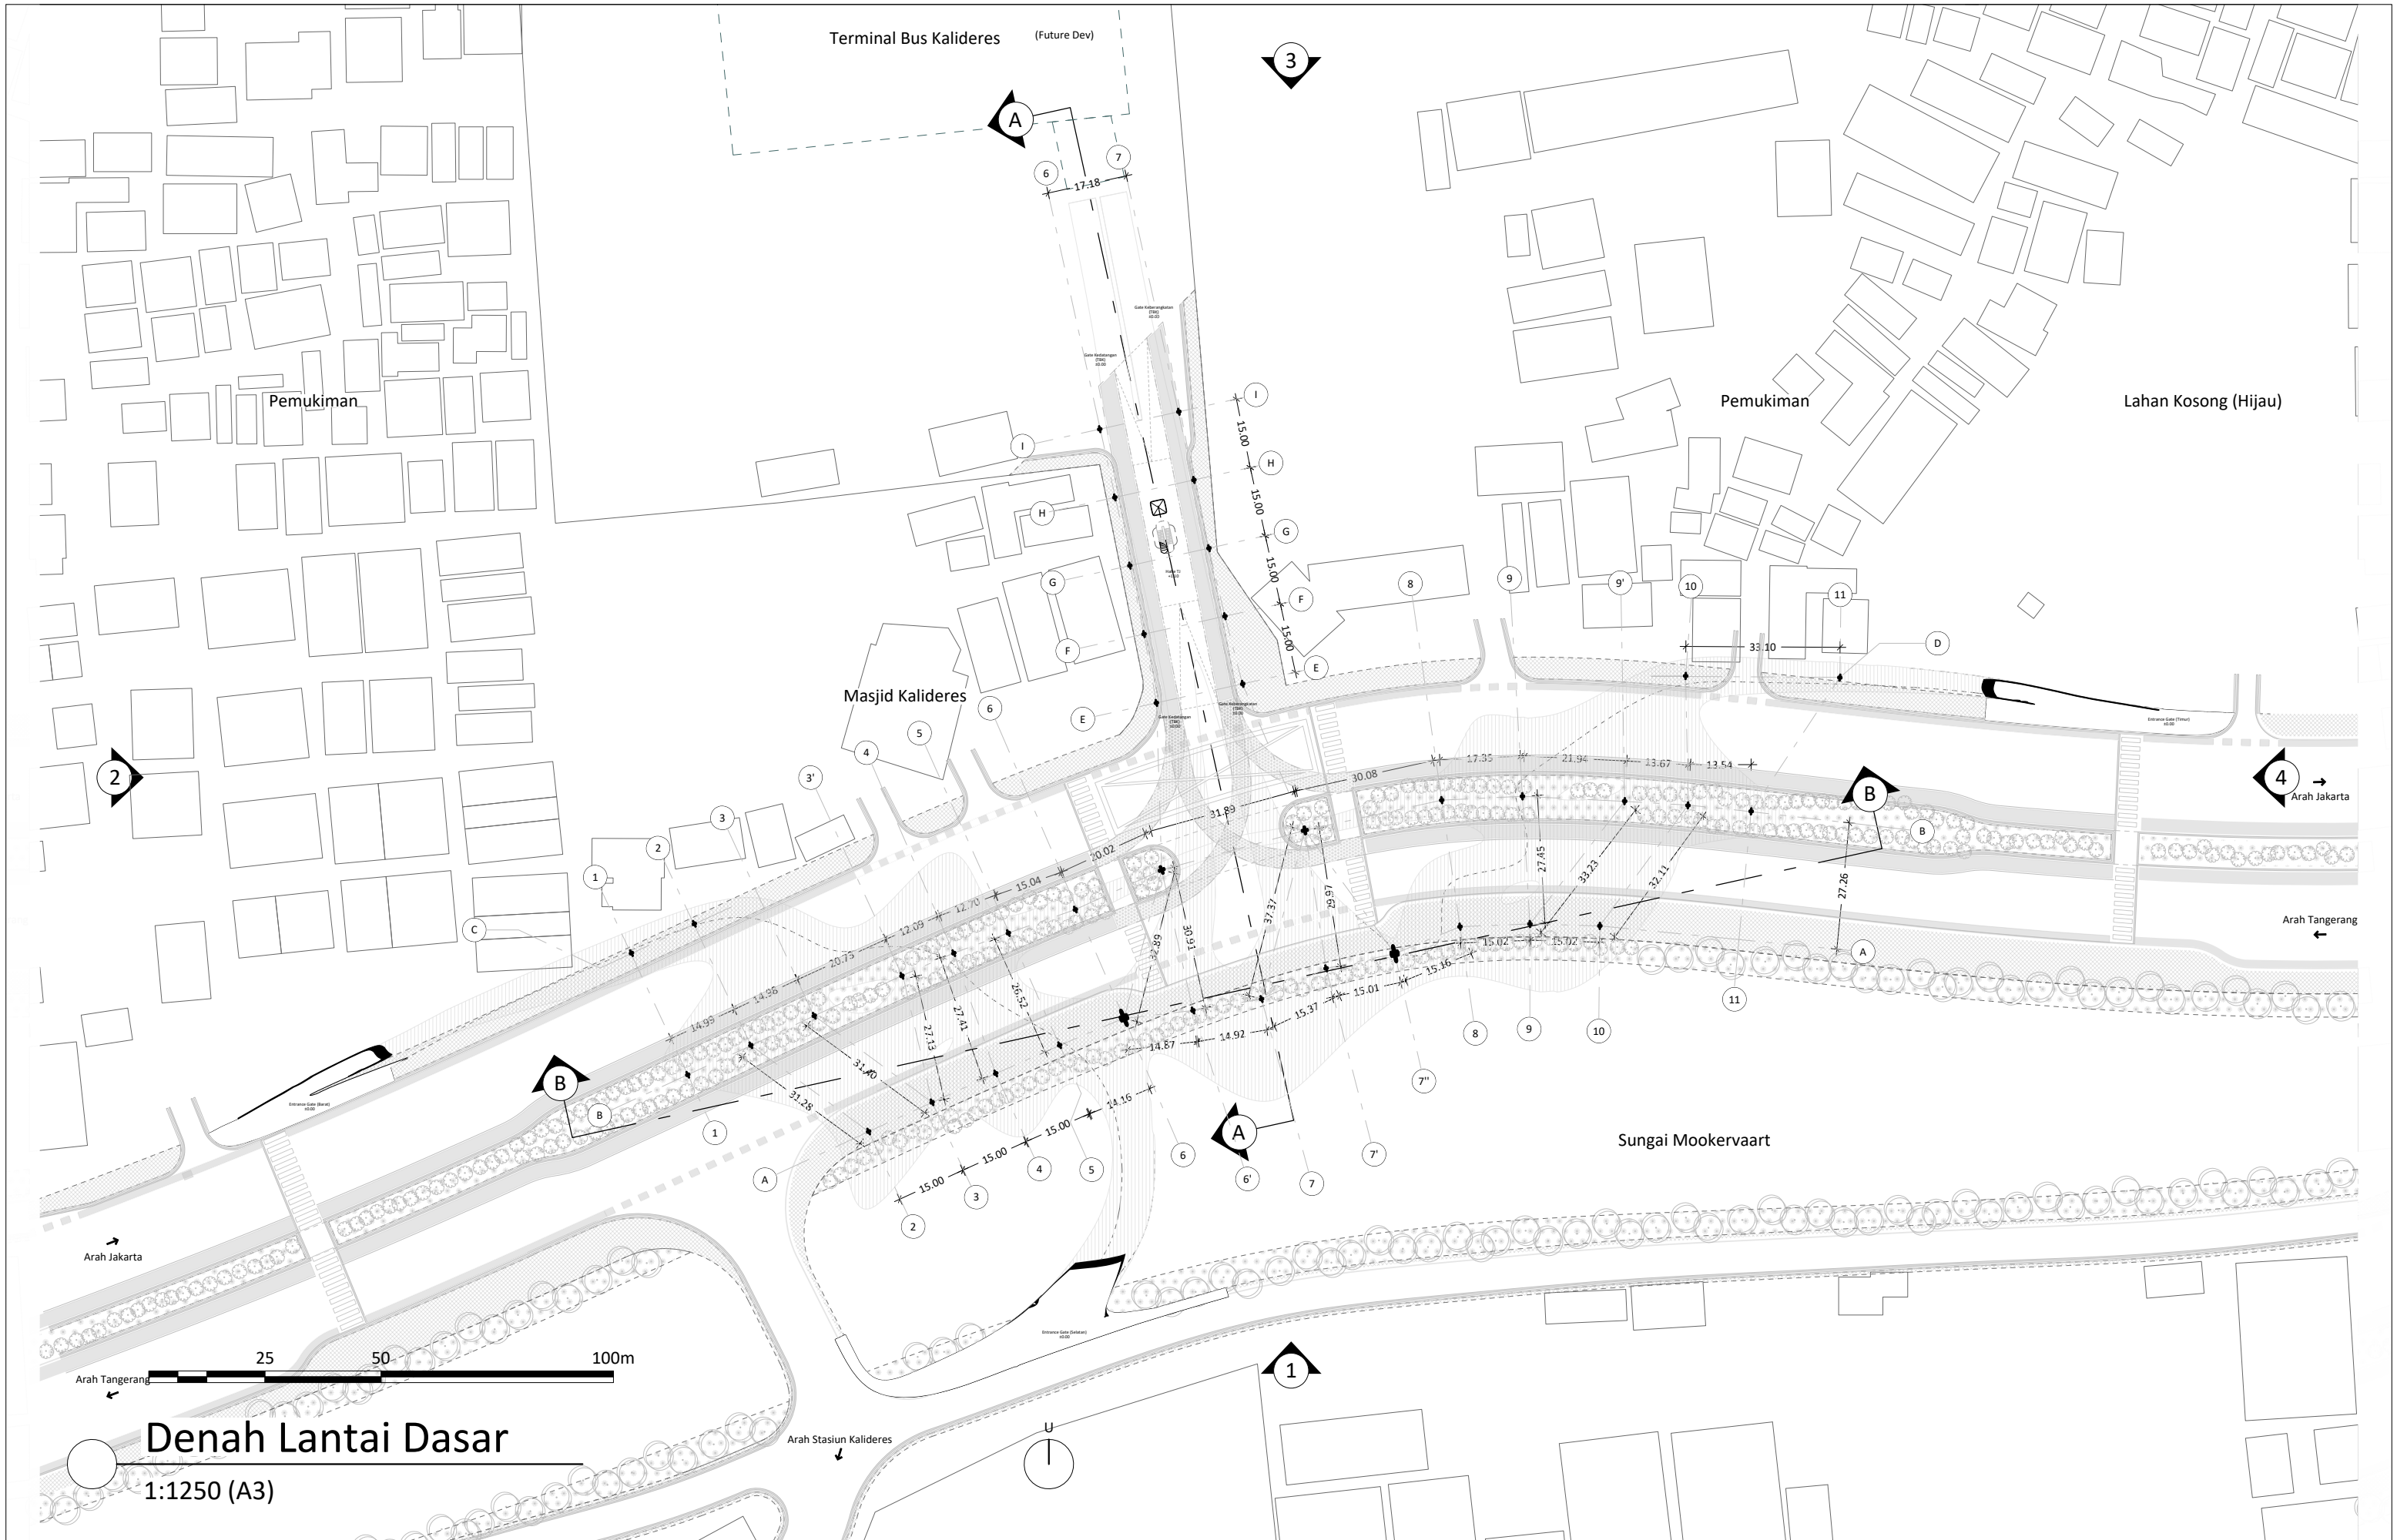

 Program Studi Magister Arsitektur Sekolah Arsitektur, Perencanaan, dan Pengembangan Kebijakan Institut Teknologi Bandung	AR6690 Tesis Semester 1 2022/2023	Kalideres Transit Hub (XTH)	Dosen Pembimbing: Aswin Indraprastha, S.T., M.T., M.Eng., Ph.D.	Nama Mahasiswa: Arnott Ferels	Tanggal: 25/01/2023
			Dosen Koordinator: Dewi Larasati, S.T, M.T, Ph.D.	NIM: 25221029	

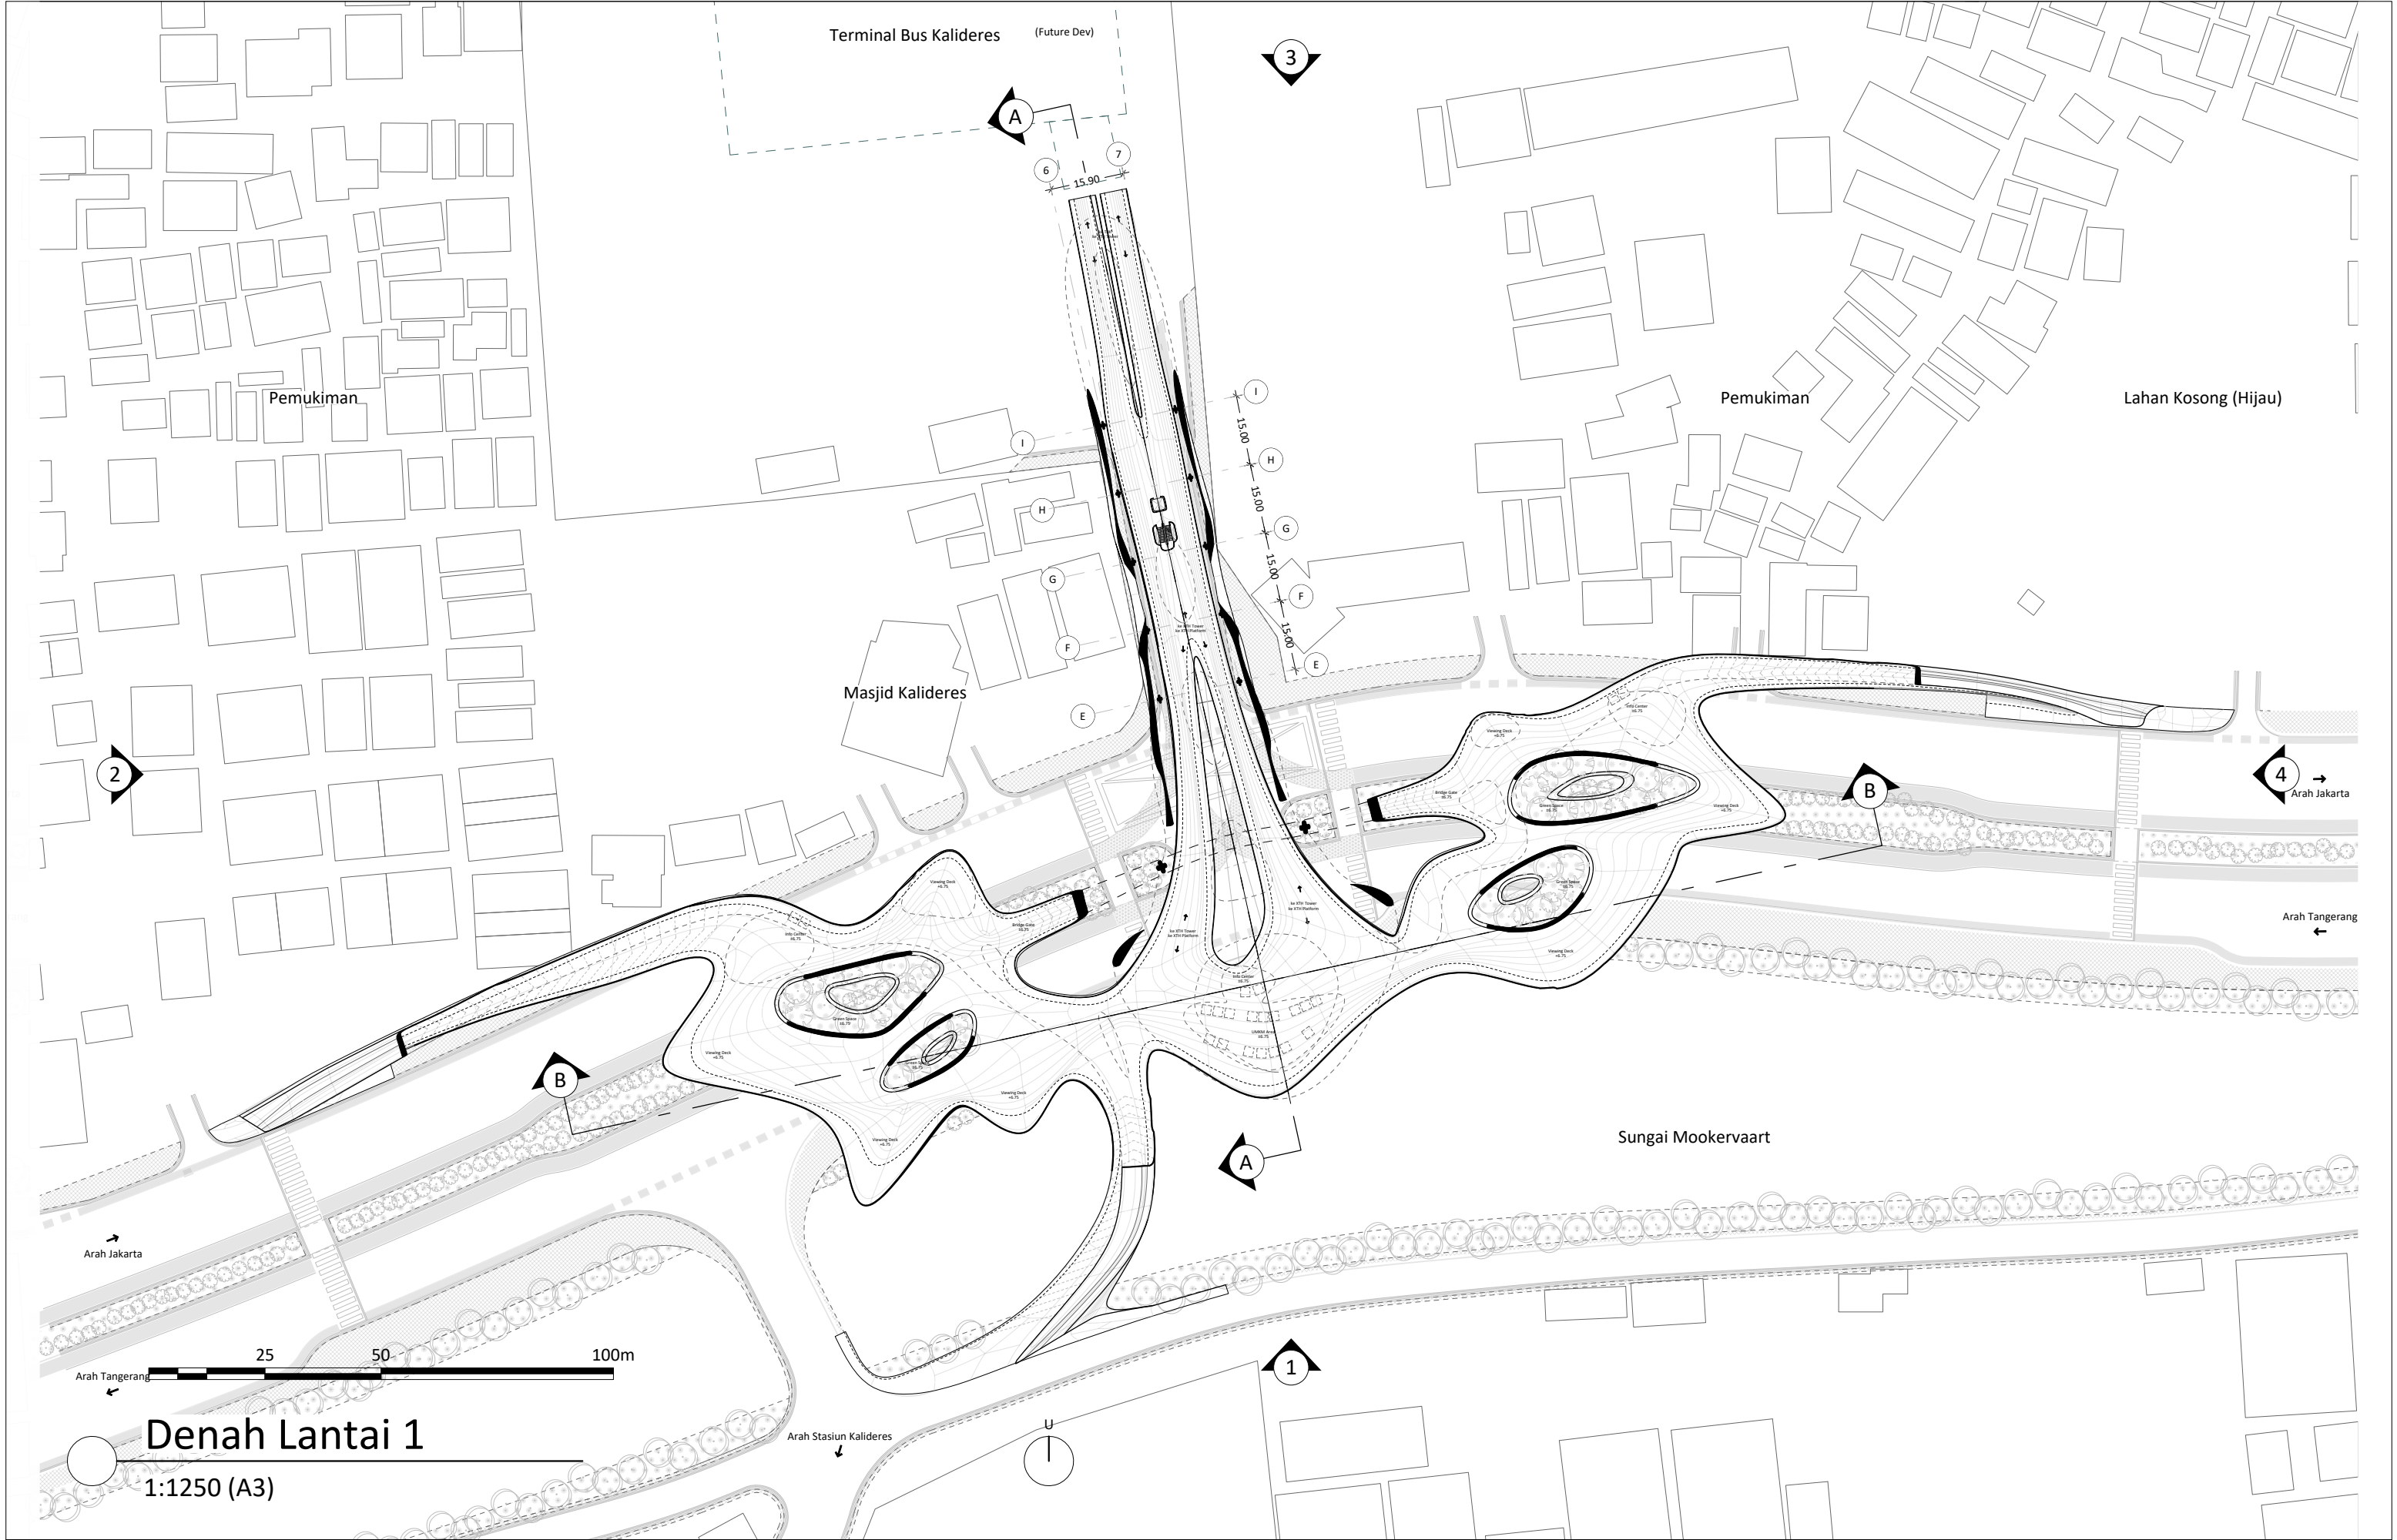

 Program Studi Magister Arsitektur Sekolah Arsitektur, Perencanaan, dan Pengembangan Kebijakan Institut Teknologi Bandung	AR6690 Tesis Semester 1 2022/2023	Kalideres Transit Hub (XTH)	Dosen Pembimbing: Aswin Indraprastha, S.T., M.T., M.Eng., Ph.D.	Nama Mahasiswa: Arnett Ferels	Tanggal: 25/01/2023
			Dosen Koordinator: Dewi Larasati, S.T, M.T, Ph.D.	NIM: 25221029	

Tampak 1 (Selatan)

1:1250 (A3)

25 50 100m



Tampak 2 (Timur)

1:1250 (A3)


25 50 100m



Tampak 3 (Utara)

1:1250 (A3)

25 50 100m


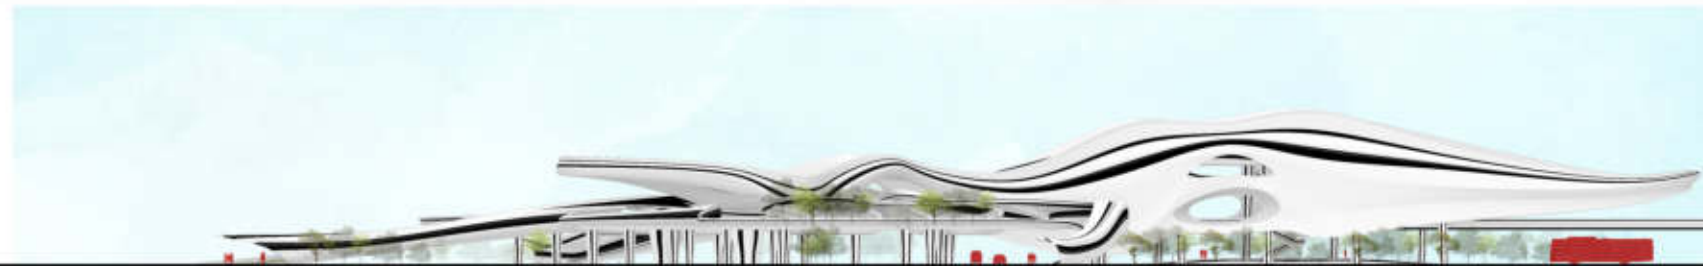



Tampak 4 (Barat)


1:1250 (A3)

25 50 100m



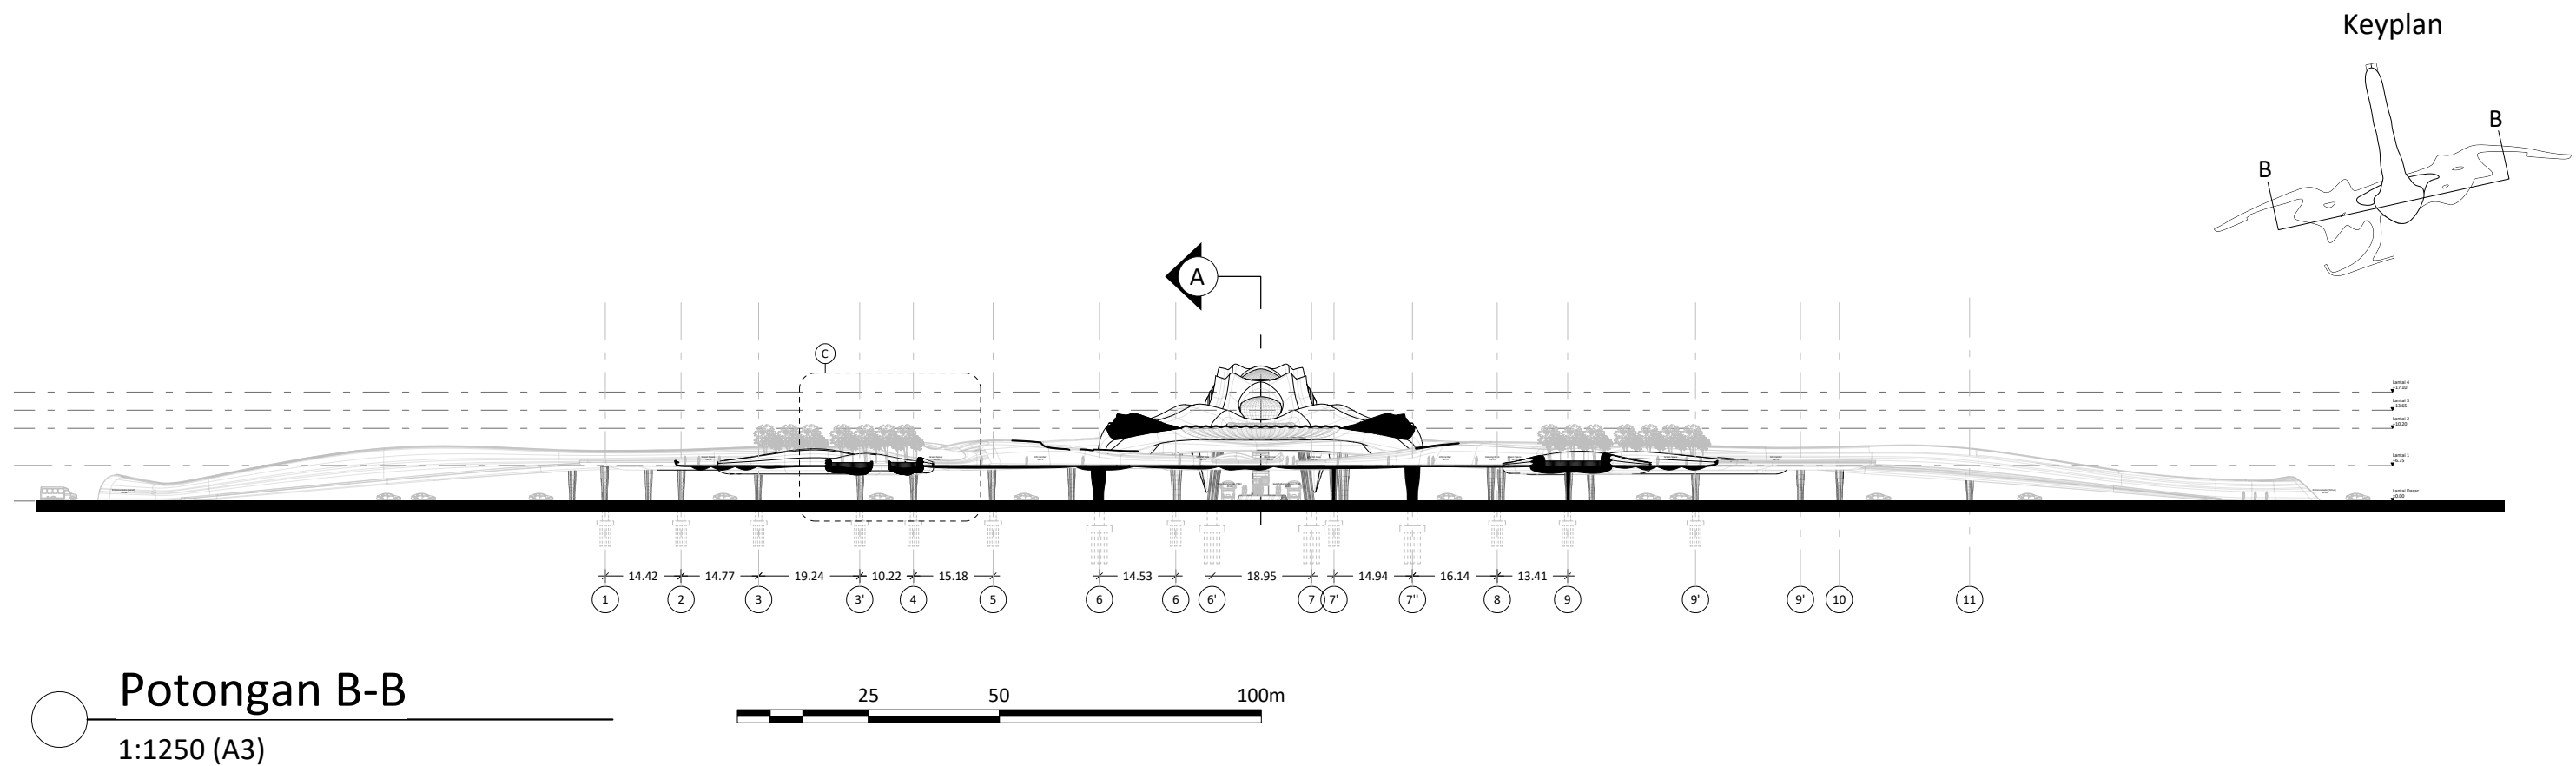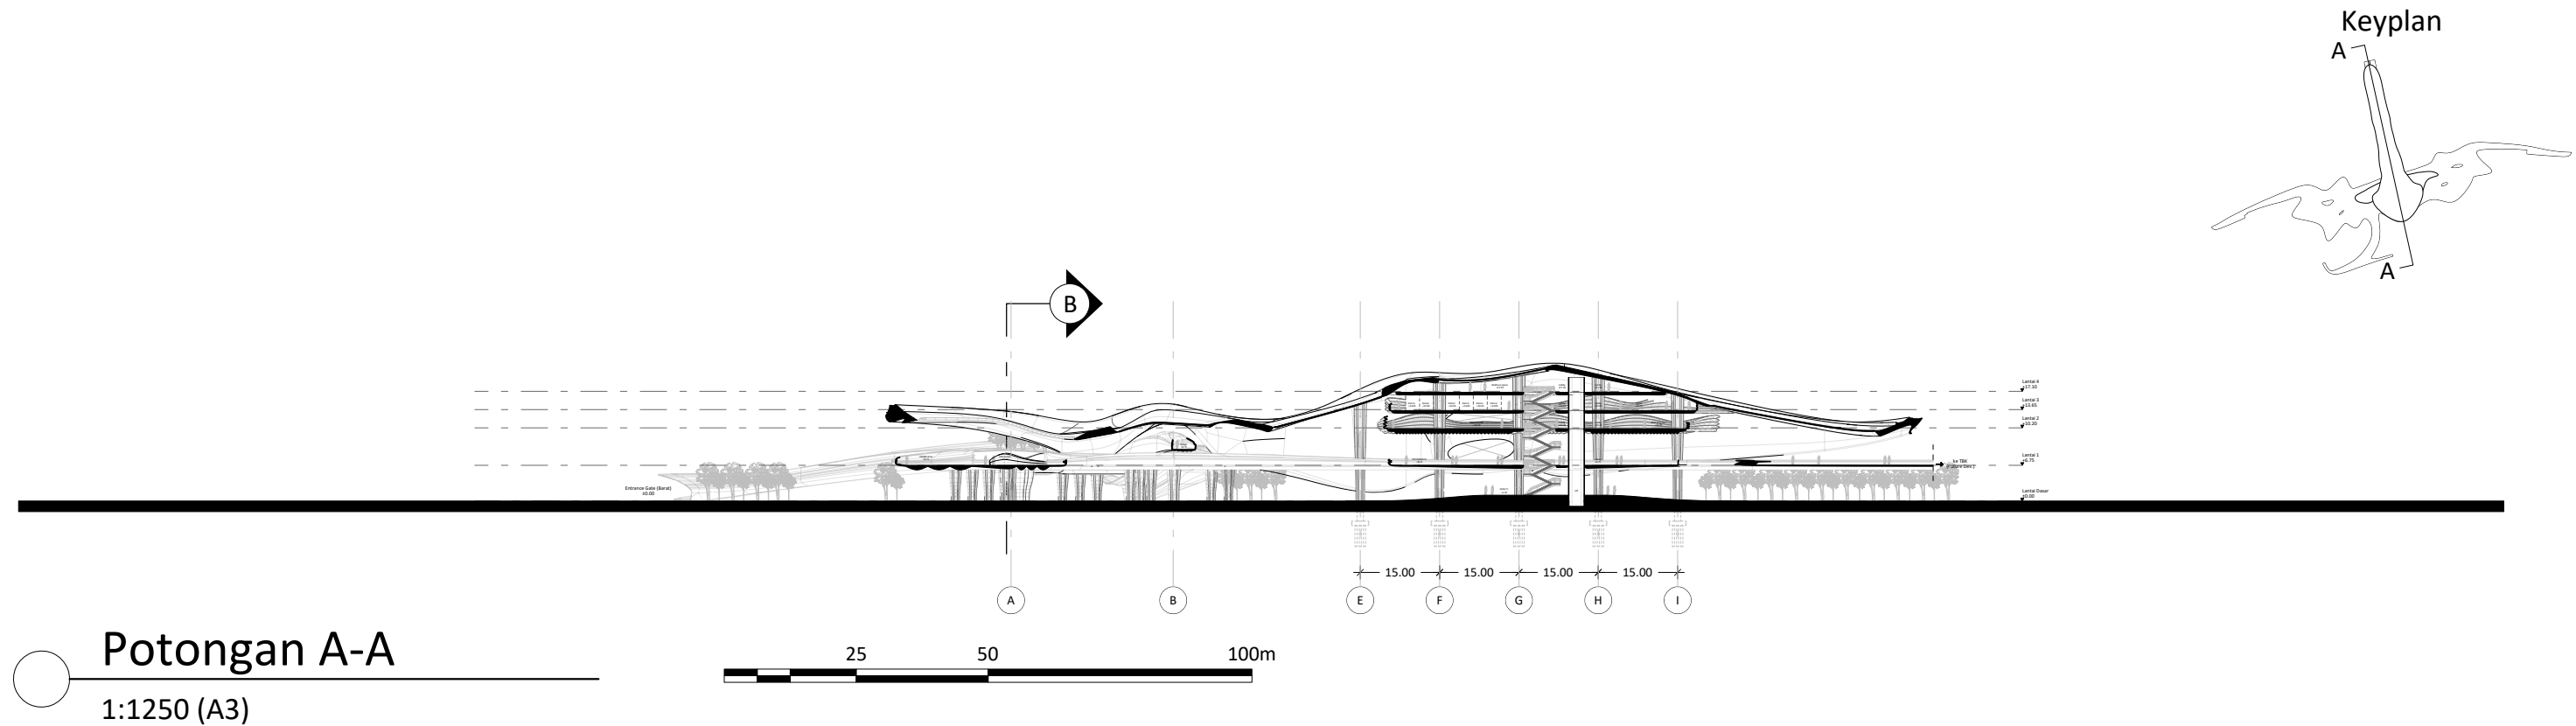

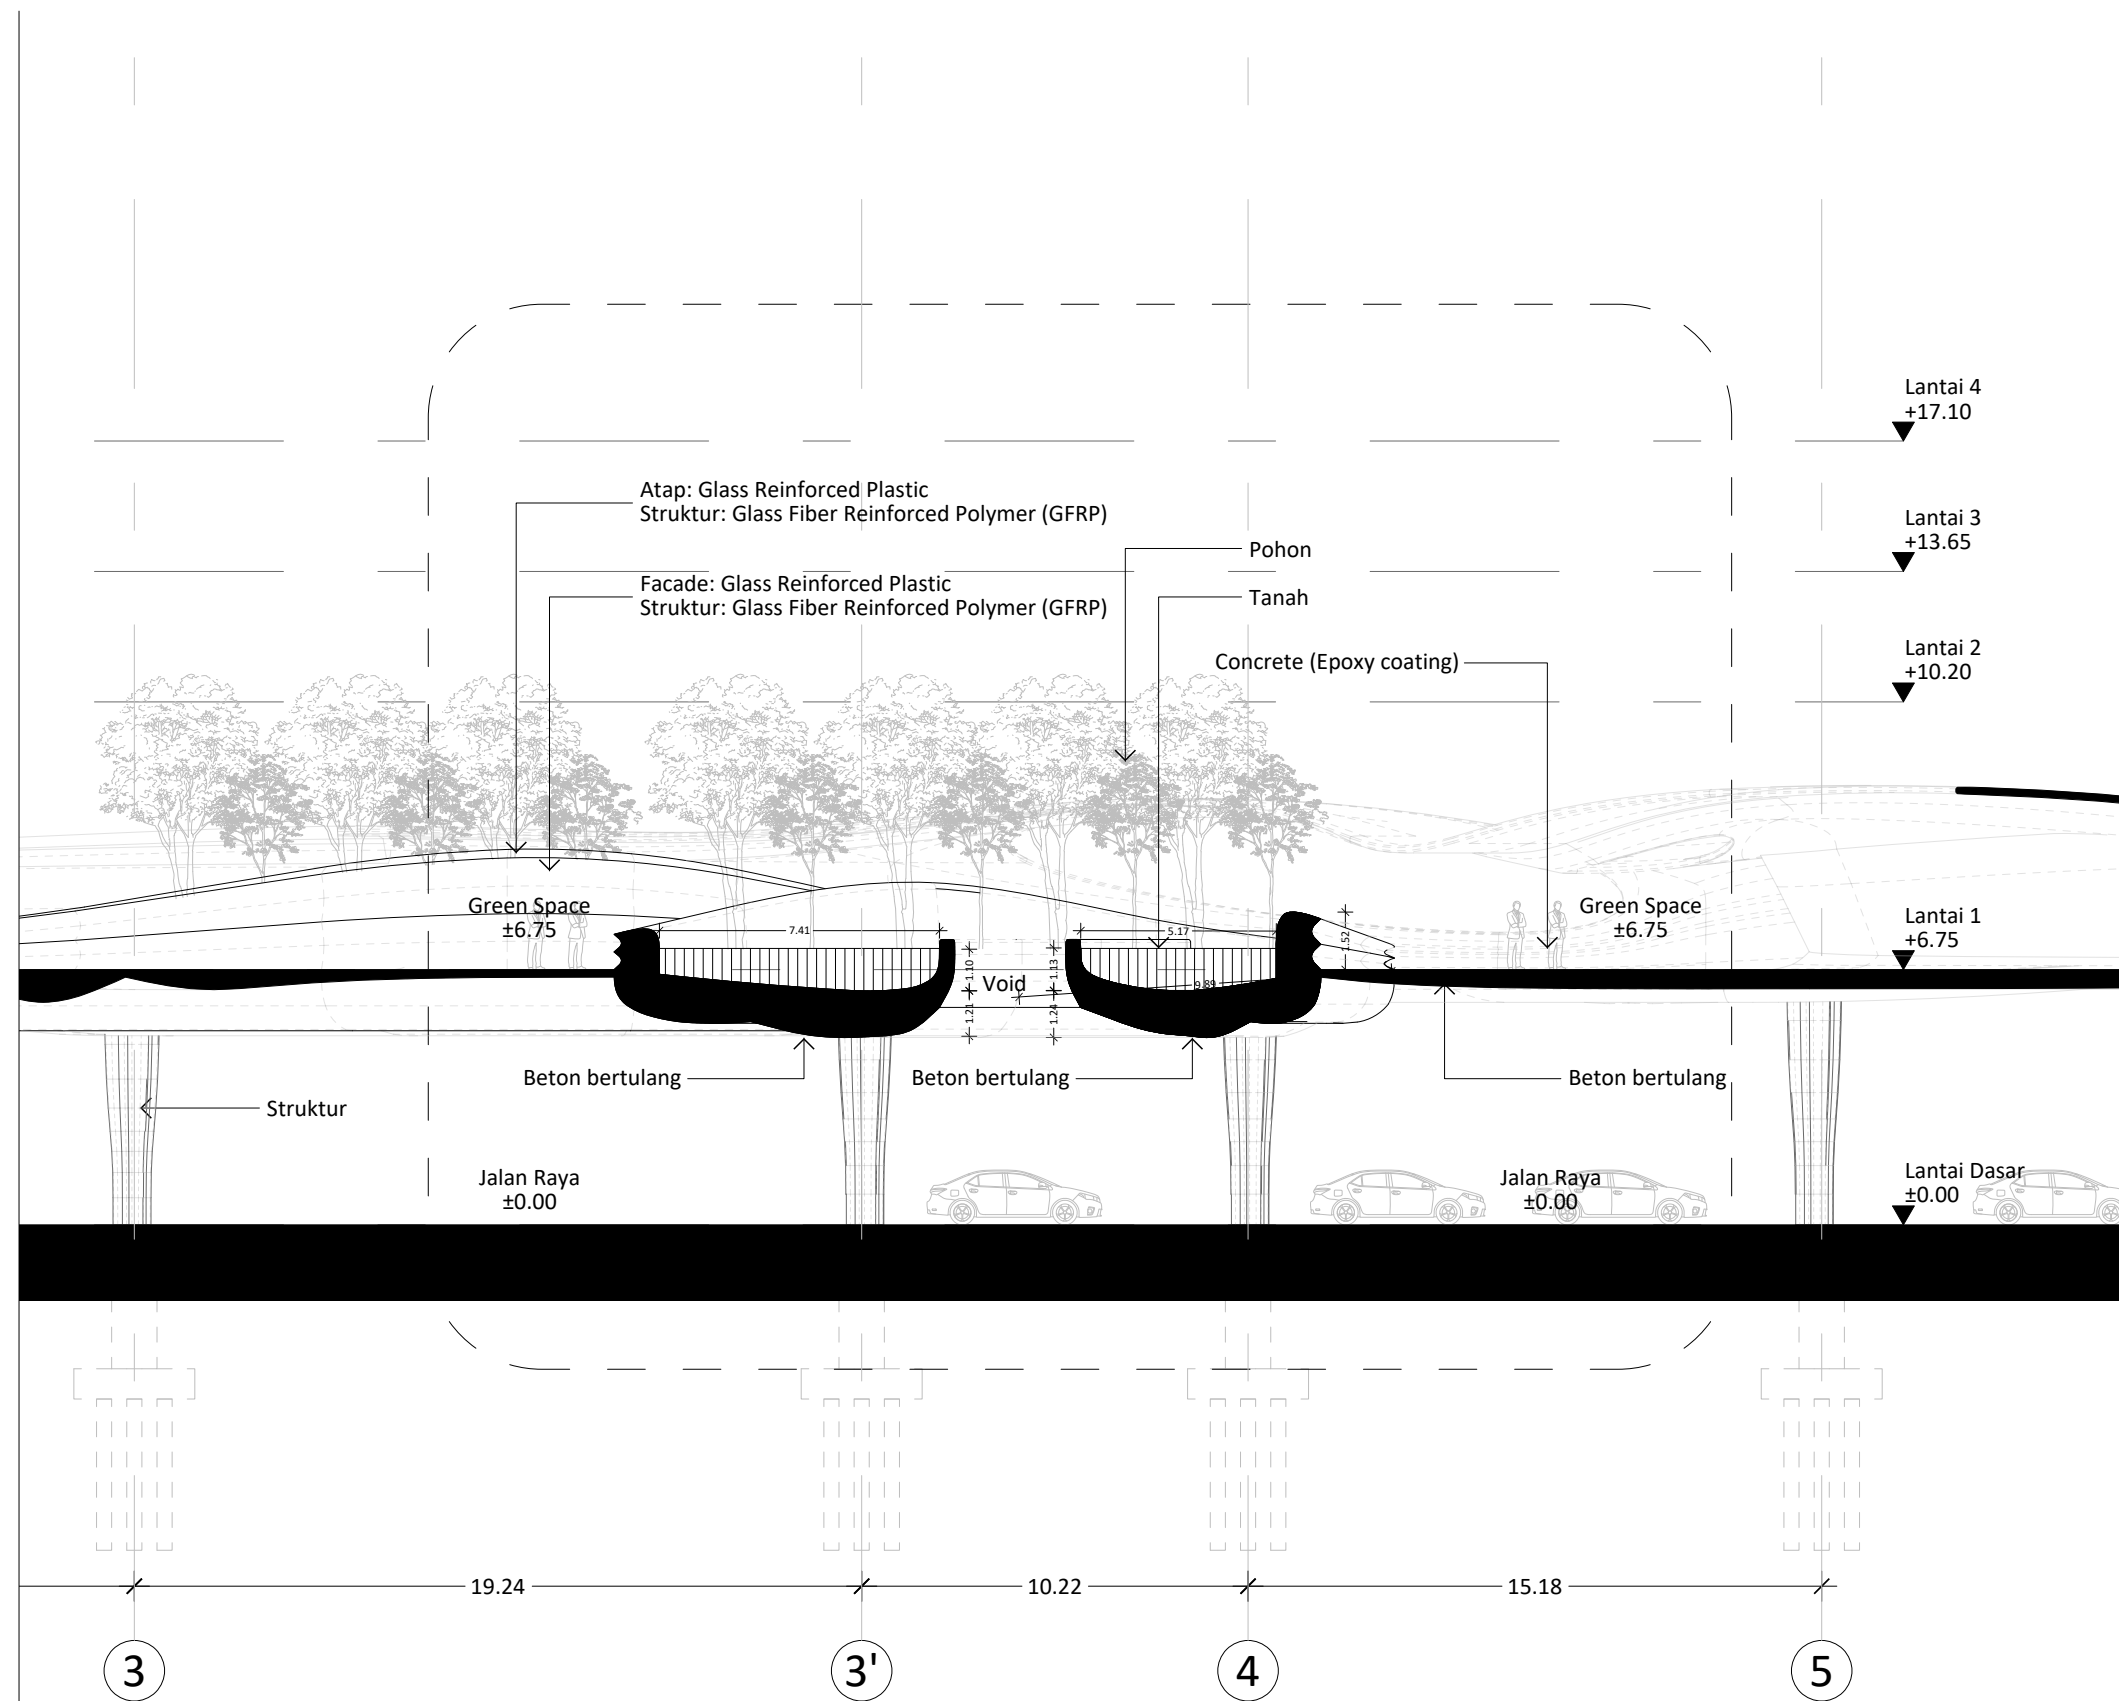

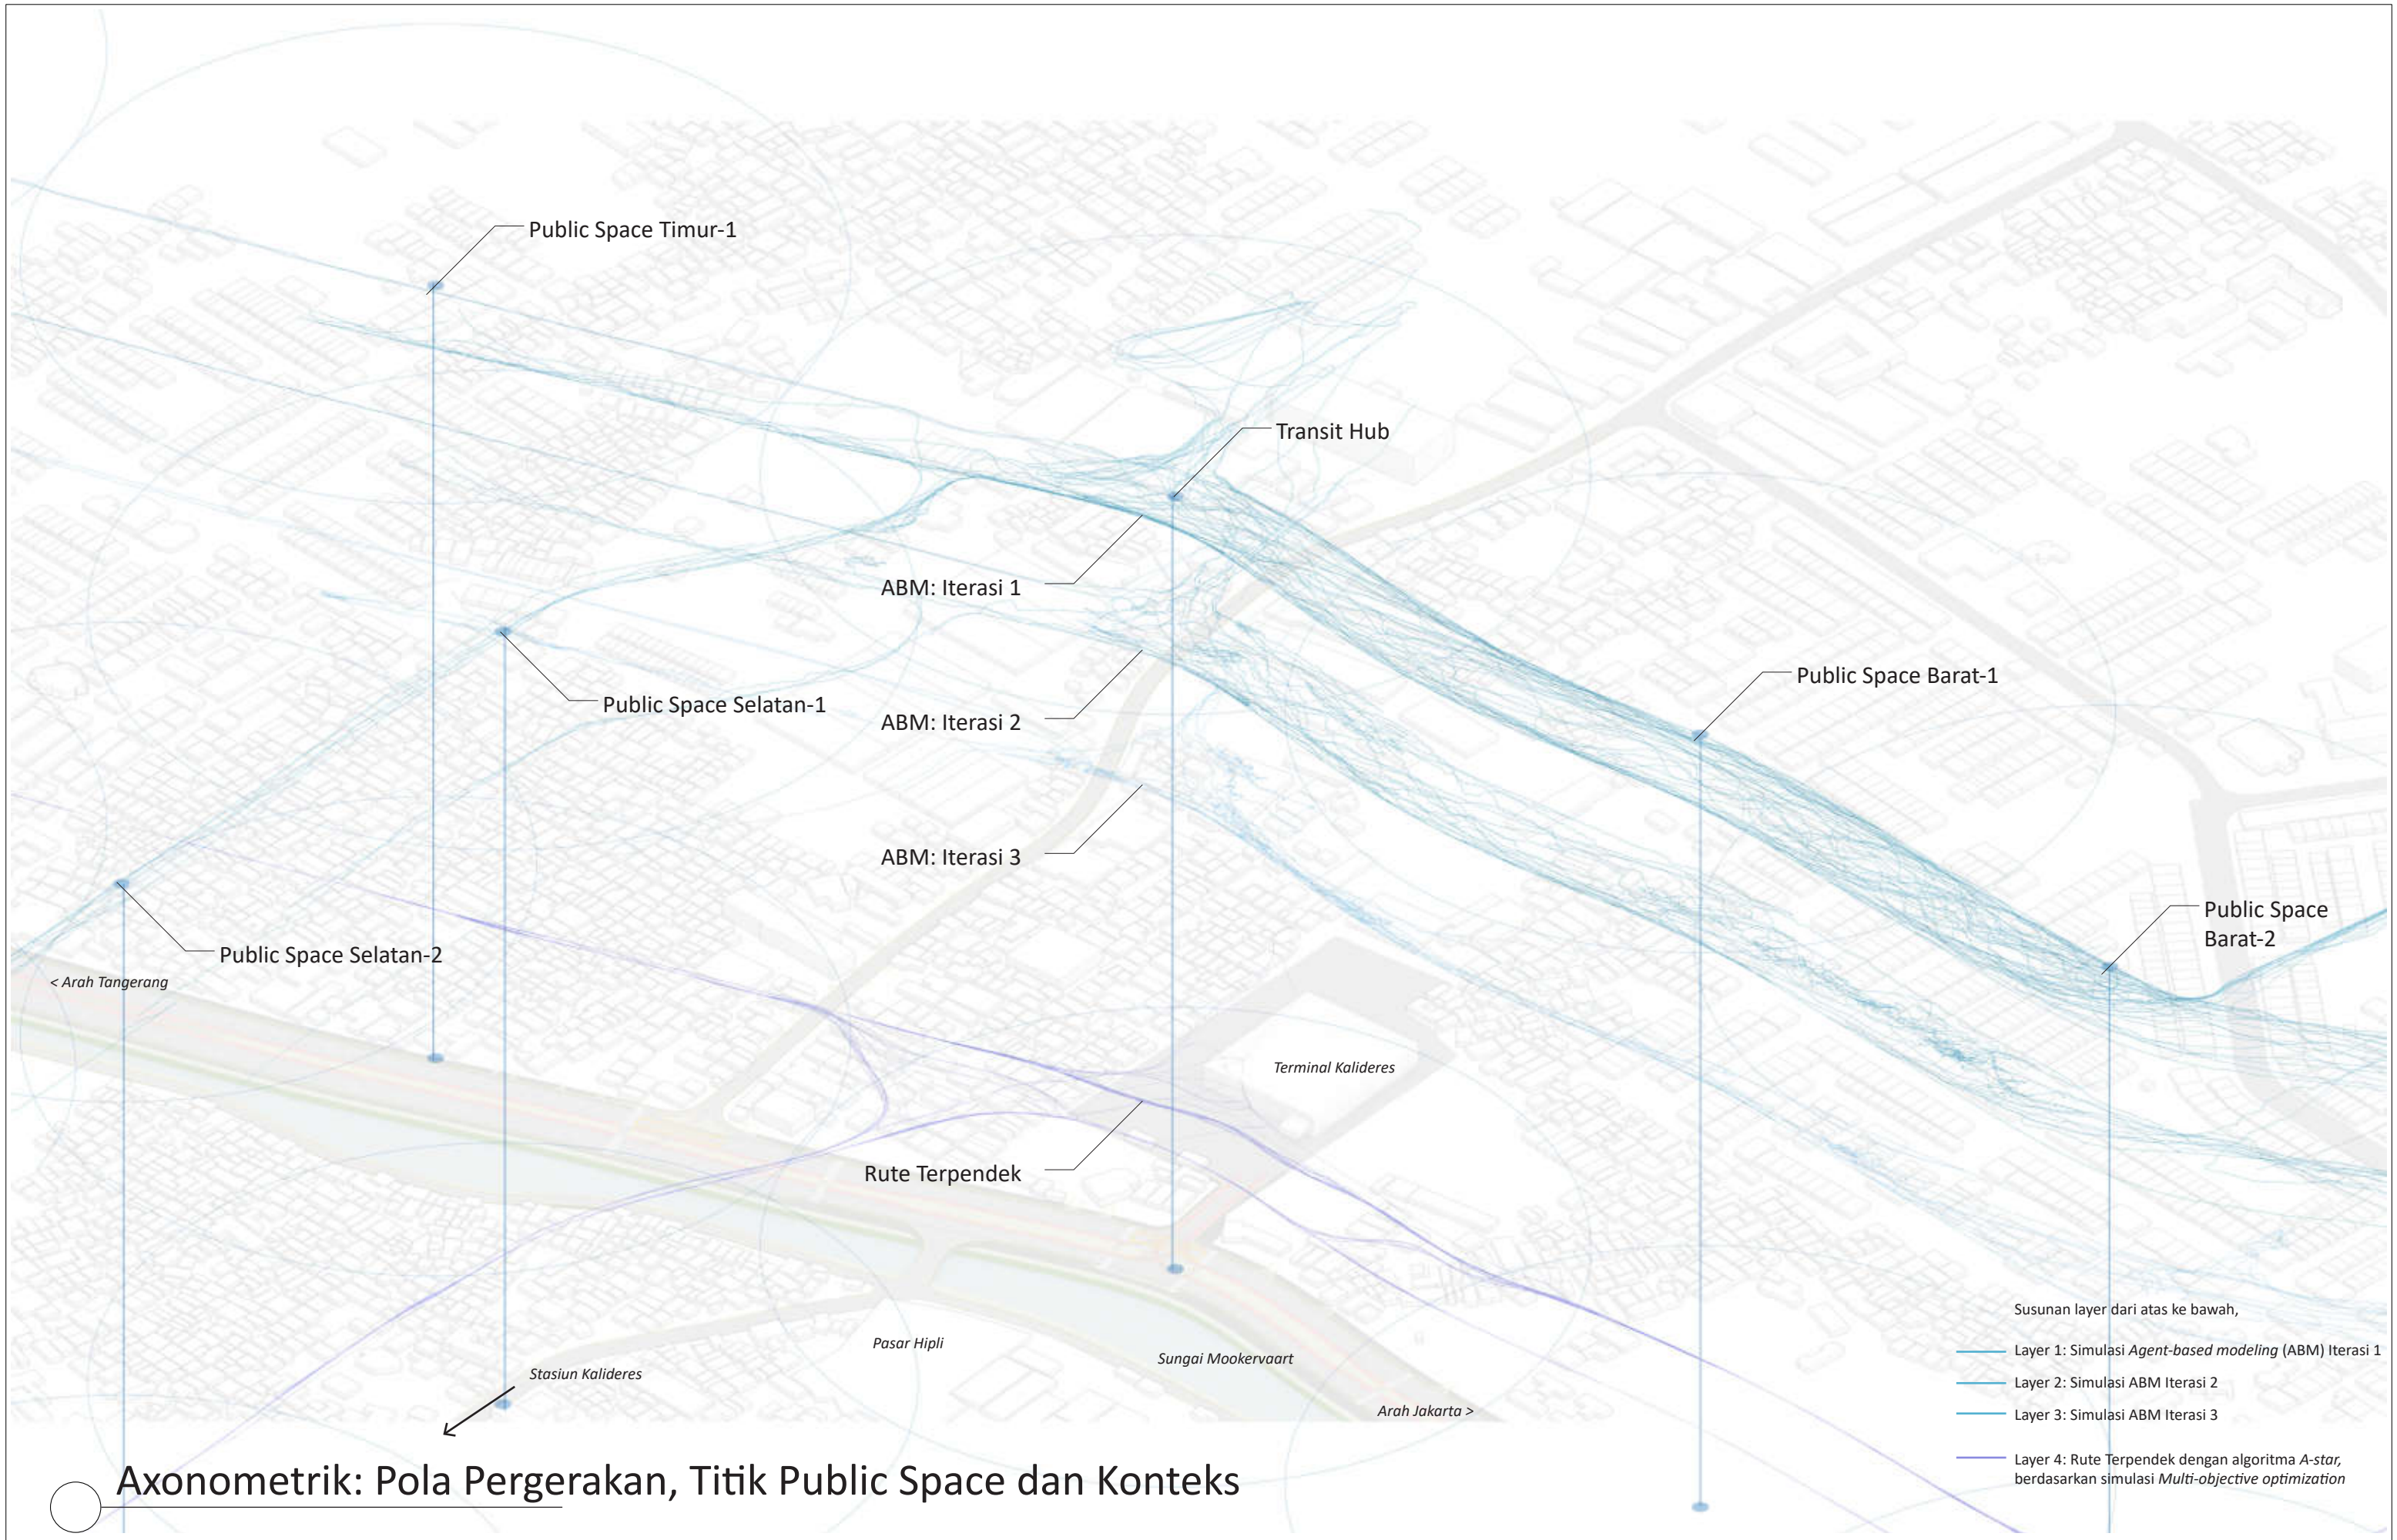

Axonometrik: Pola Pergerakan, Titik Public Space dan Konteks



Program Studi Magister Arsitektur
Sekolah Arsitektur, Perencanaan, dan Pengembangan Kebijakan
Institut Teknologi Bandung

AR6690 Tesis
Semester 1 2022/2023

Kalideres Transit Hub (XTH)


Dosen Pembimbing:
Aswin Indraprastha, S.T., M.T., M.Eng., Ph.D.

Dosen Koordinator:
Dewi Larasati, S.T, M.T, Ph.D.

Nama Mahasiswa:
Arnott Ferels

NIM:
25221029

Tanggal:
25/01/2023

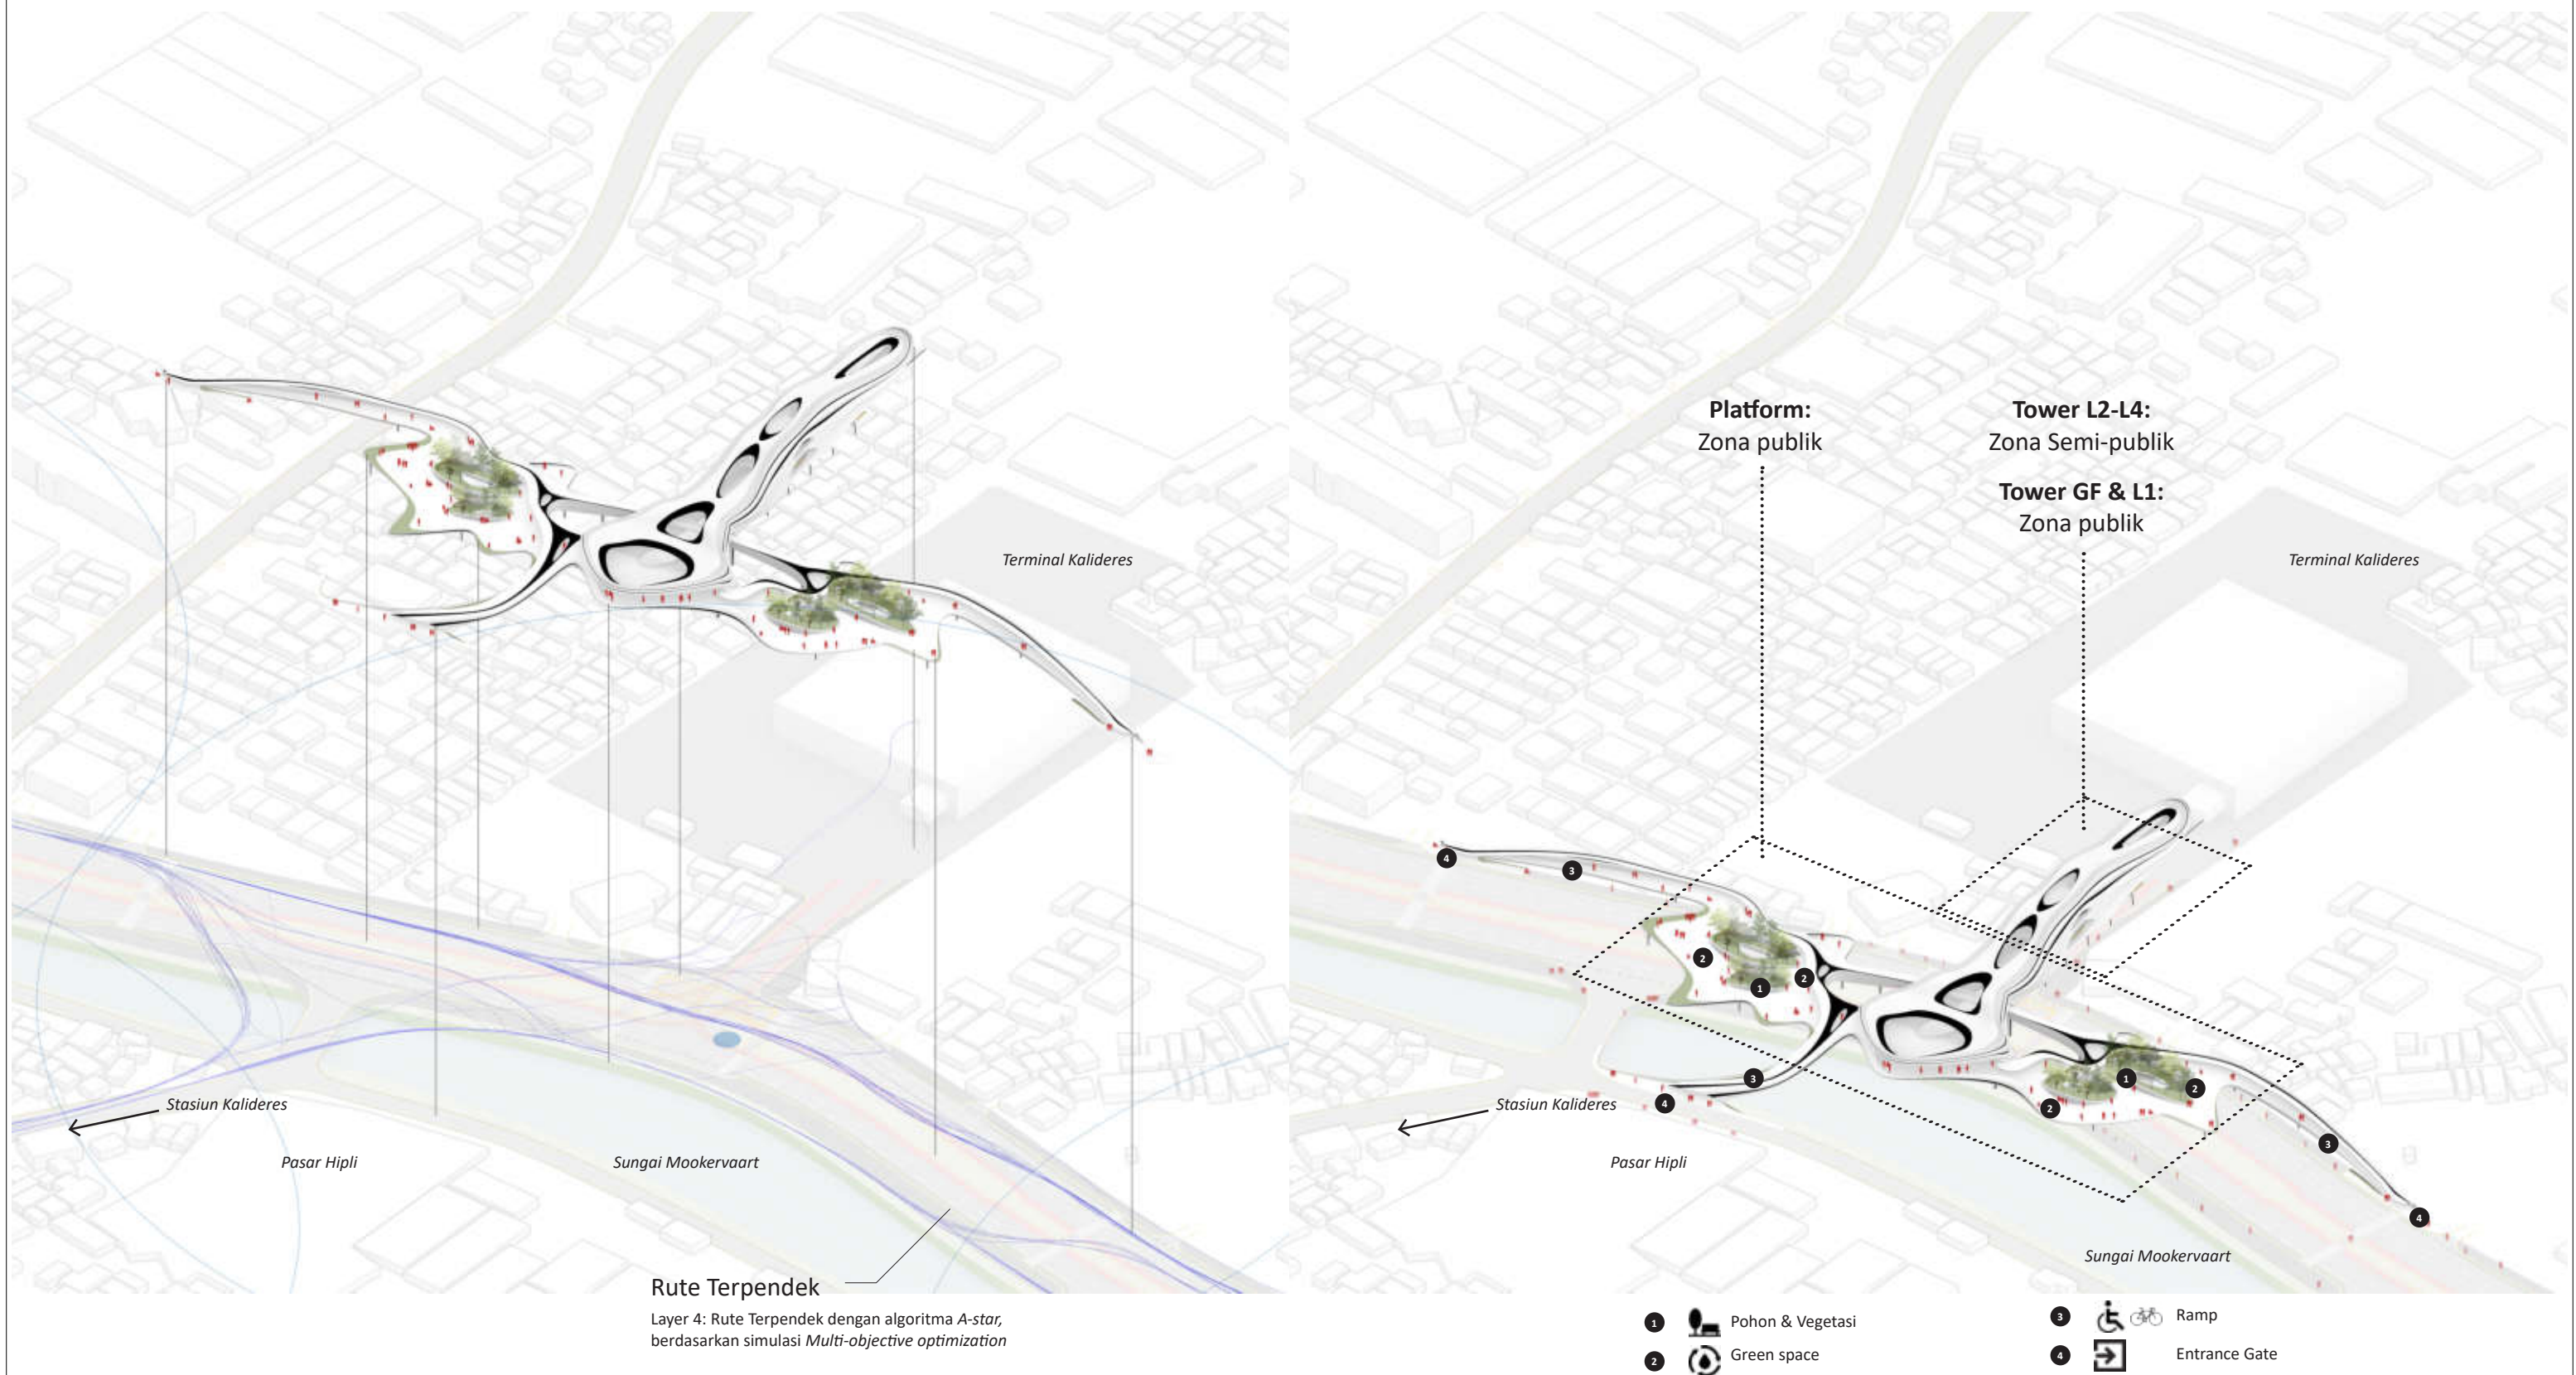

Axonometrik: Pola Pergerakan dan Konteks terhadap Desain



Program Studi Magister Arsitektur
Sekolah Arsitektur, Perencanaan, dan Pengembangan Kebijakan
Institut Teknologi Bandung

AR6690 Tesis
Semester 1 2022/2023

Kalideres Transit Hub (XTH)


Dosen Pembimbing:
Aswin Indraprastha, S.T., M.T., M.Eng., Ph.D.

Dosen Koordinator:
Dewi Larasati, S.T, M.T, Ph.D.


Nama Mahasiswa:
Arnett Ferels

NIM:
25221029

Tanggal:
25/01/2023

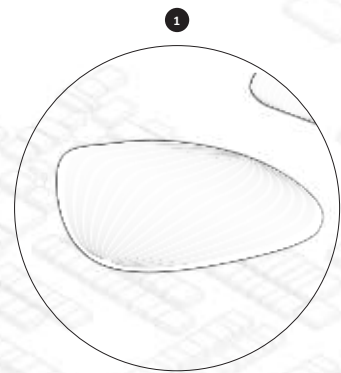


1

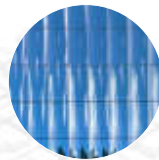

Prefab tempered glass



Prefab long-span steel structure

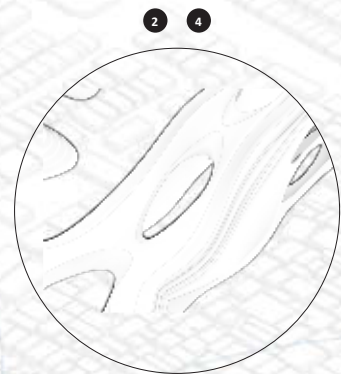

2


4



GRP



GFRP

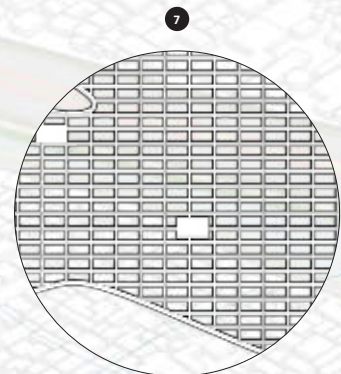


7



Waffle slab



Waffle slab

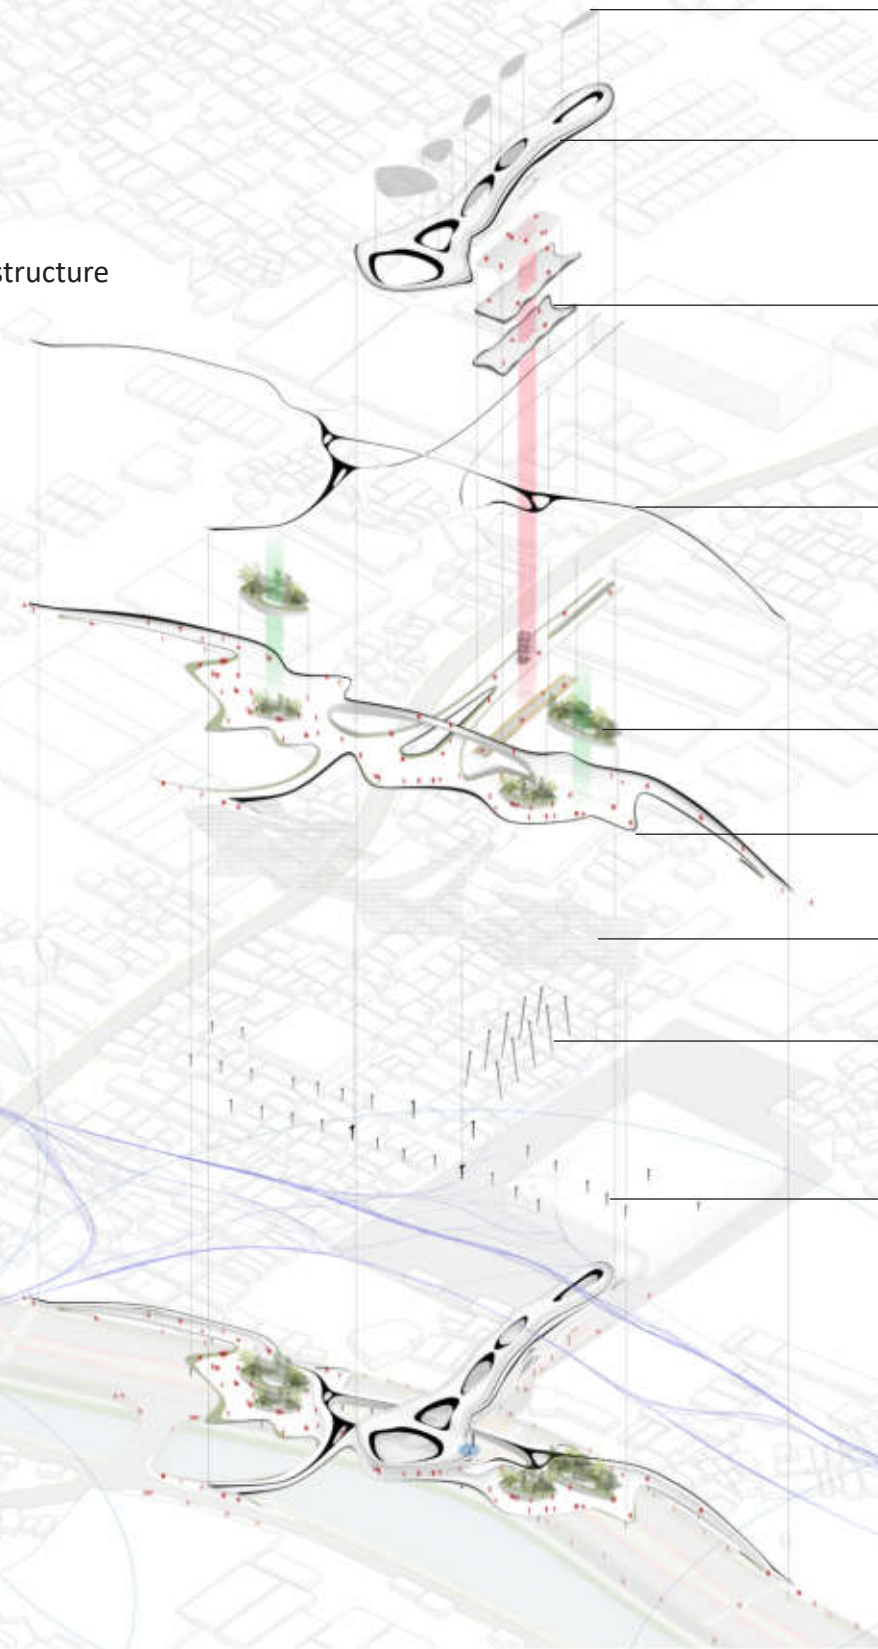

1 Finishing atap: **Prefab tempered glass**
Struktur atap: **Prefab long-span steel structure**

2 Finishing facade eksterior: **Fiberglass Reinforced Plastic prefab panels (GRP)**.
Finishing facade Interior: **Fiberglass Reinforced Plastic prefab panels (GRP)**.
Struktur facade: **Glass Fiber Reinforced Polymer (GFRP)**.

3 Struktur plat lantai: **Beton bertulang**.
Finishing plat lantai: **Concrete (Epoxy coating)**.

4 Finishing facade eksterior: **Fiberglass Reinforced Plastic prefab panels (GRP)**.
Finishing facade Interior: **Fiberglass Reinforced Plastic prefab panels (GRP)**.
Struktur facade: **Glass Fiber Reinforced Polymer (GFRP)**.

1 Struktur penopang Green Space : **Beton bertulang** (tebal min 1 m).
Finishing Green Space : **Concrete (Epoxy coating)**.

6 Struktur plat lantai: **Beton bertulang**.
Finishing plat lantai: **Concrete (Epoxy coating)**.

7 Struktur plat platform : **beton bertulang**
Model : **Waffle slab** (rusuk beton bertulang dua arah).

8 Struktur penopang XTH Tower : **beton bertulang**
Model : **Kolom Slanted**

9 Struktur penopang XTH Platform: **beton bertulang**
Model : **Kolom tegak lurus**

Axonometrik: Desain Struktur & Material



Program Studi Magister Arsitektur
Sekolah Arsitektur, Perencanaan, dan Pengembangan Kebijakan
Institut Teknologi Bandung

AR6690 Tesis
Semester 1 2022/2023

Kalideres Transit Hub (XTH)


Dosen Pembimbing:
Aswin Indraprastha, S.T., M.T., M.Eng., Ph.D.


Dosen Koordinator:
Dewi Larasati, S.T, M.T, Ph.D.

Nama Mahasiswa:
Arnett Ferels

NIM:
25221029



Tanggal:
25/01/2023

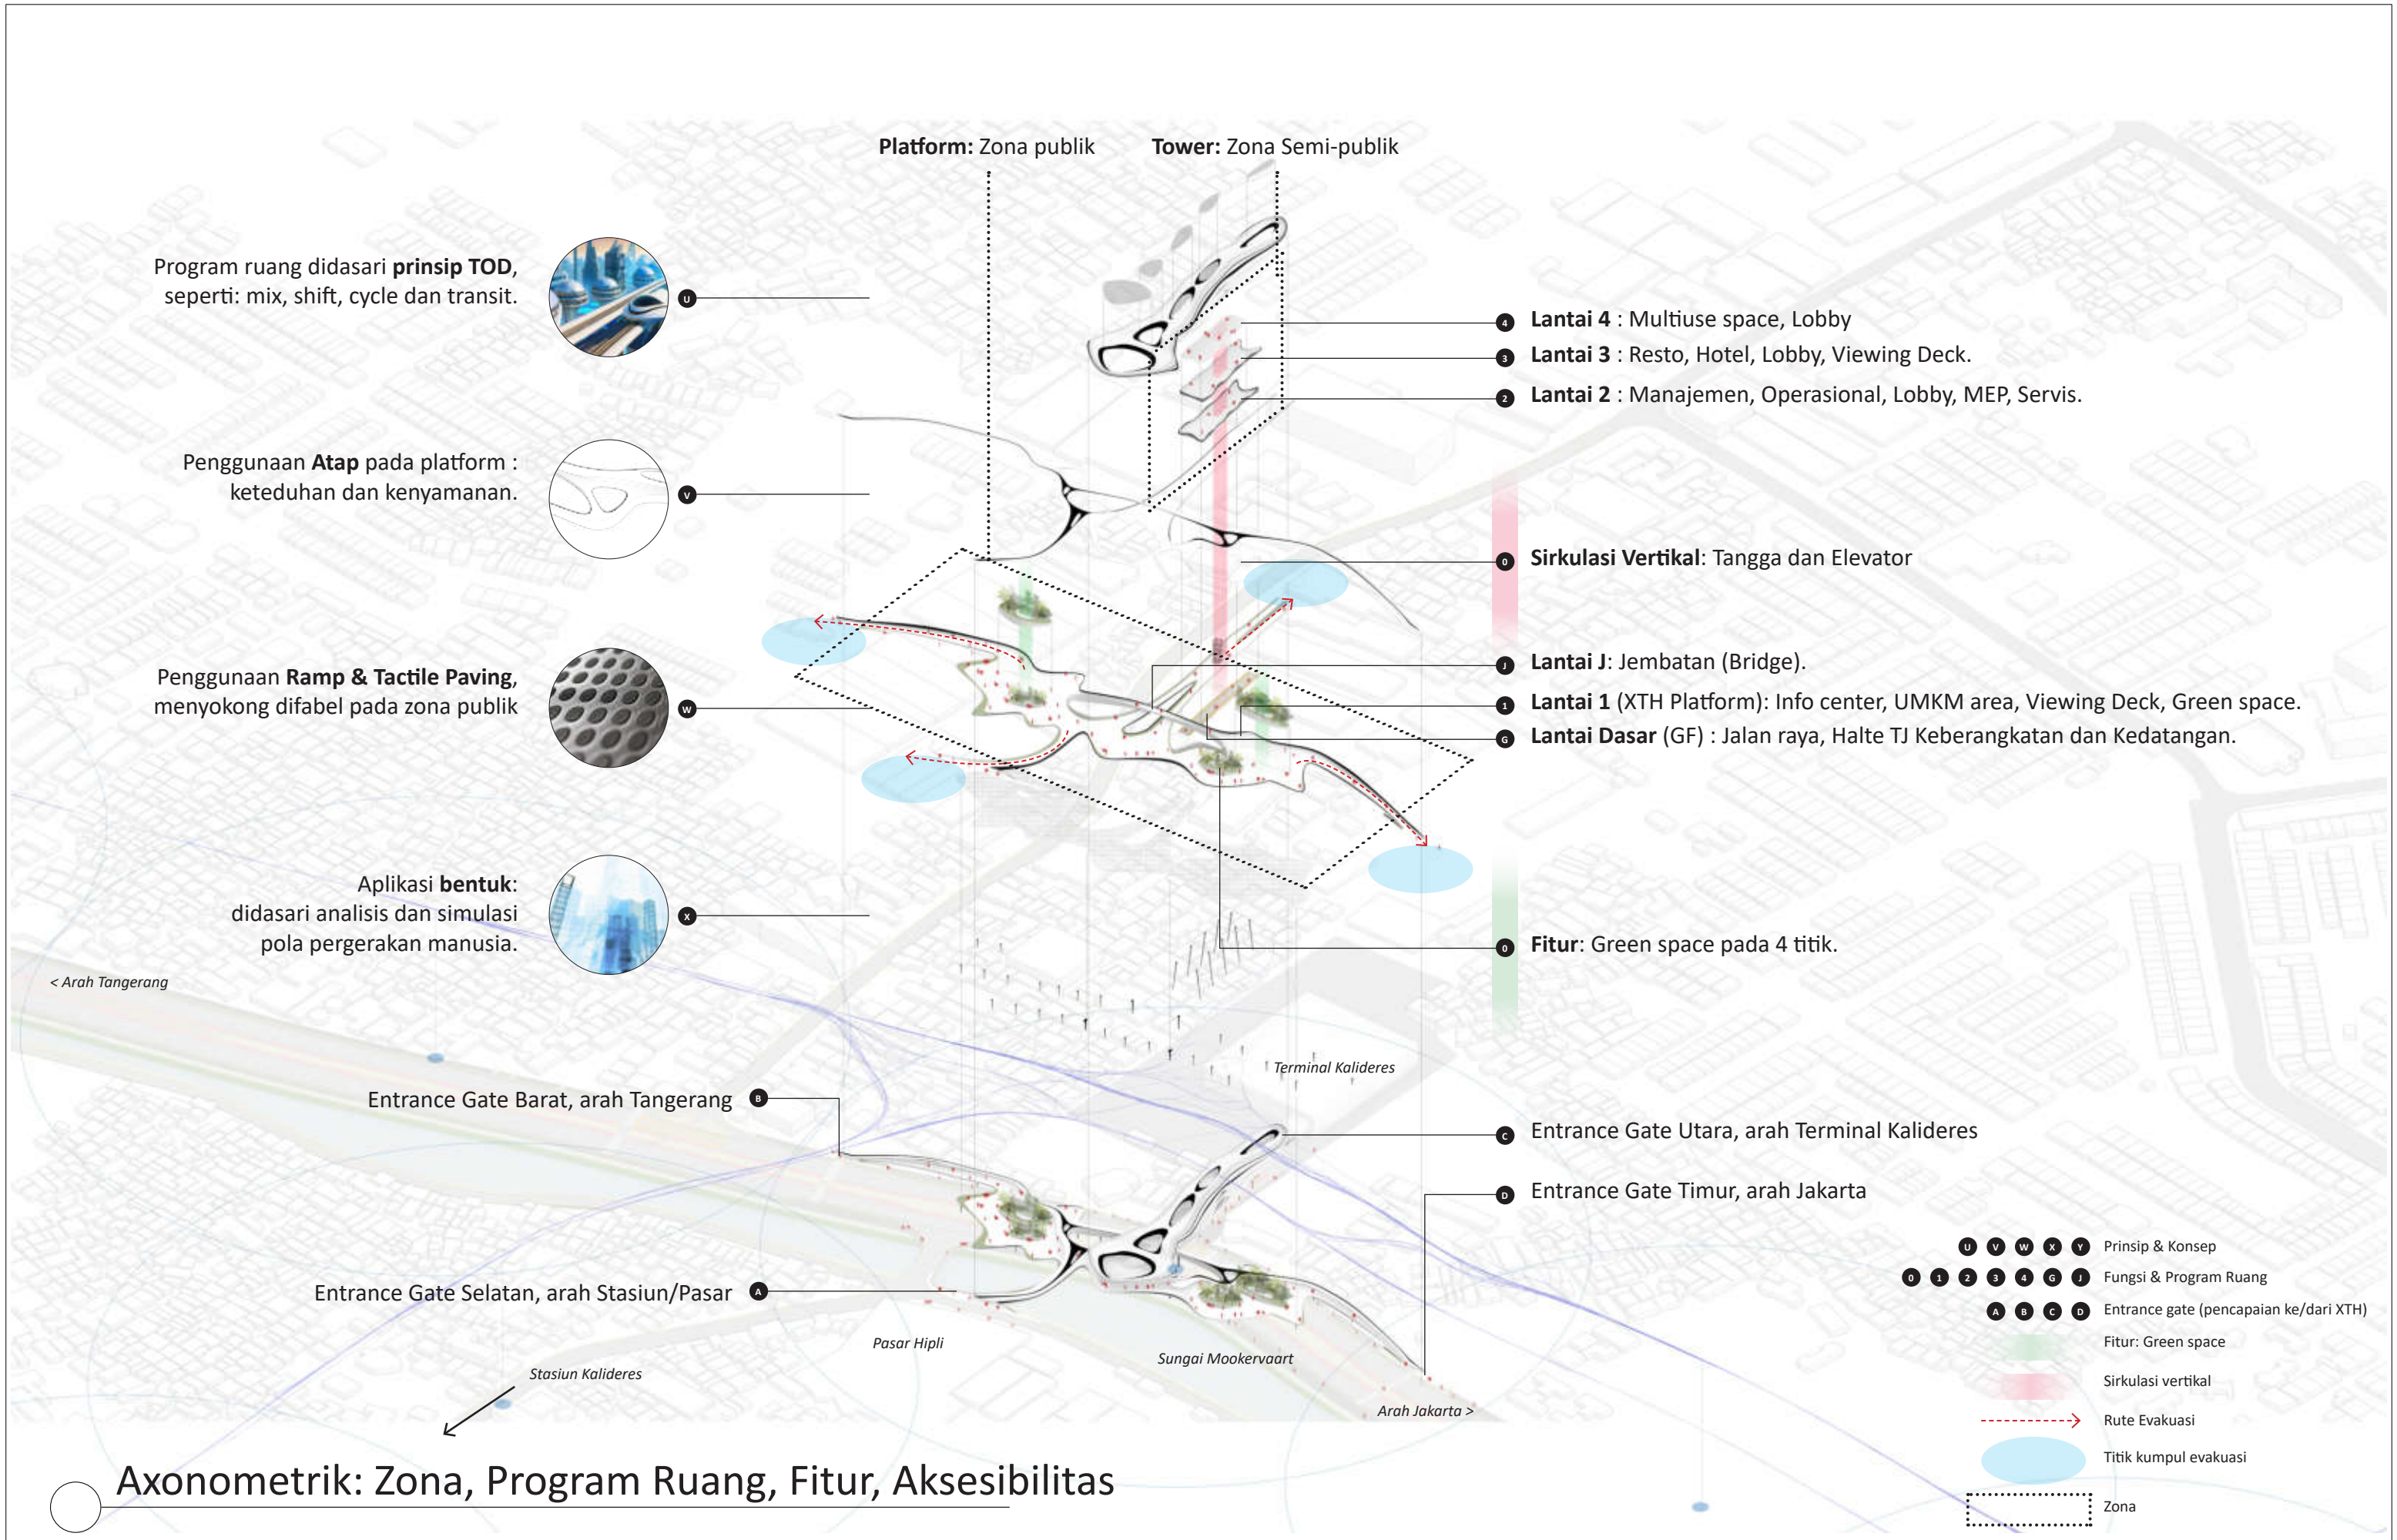


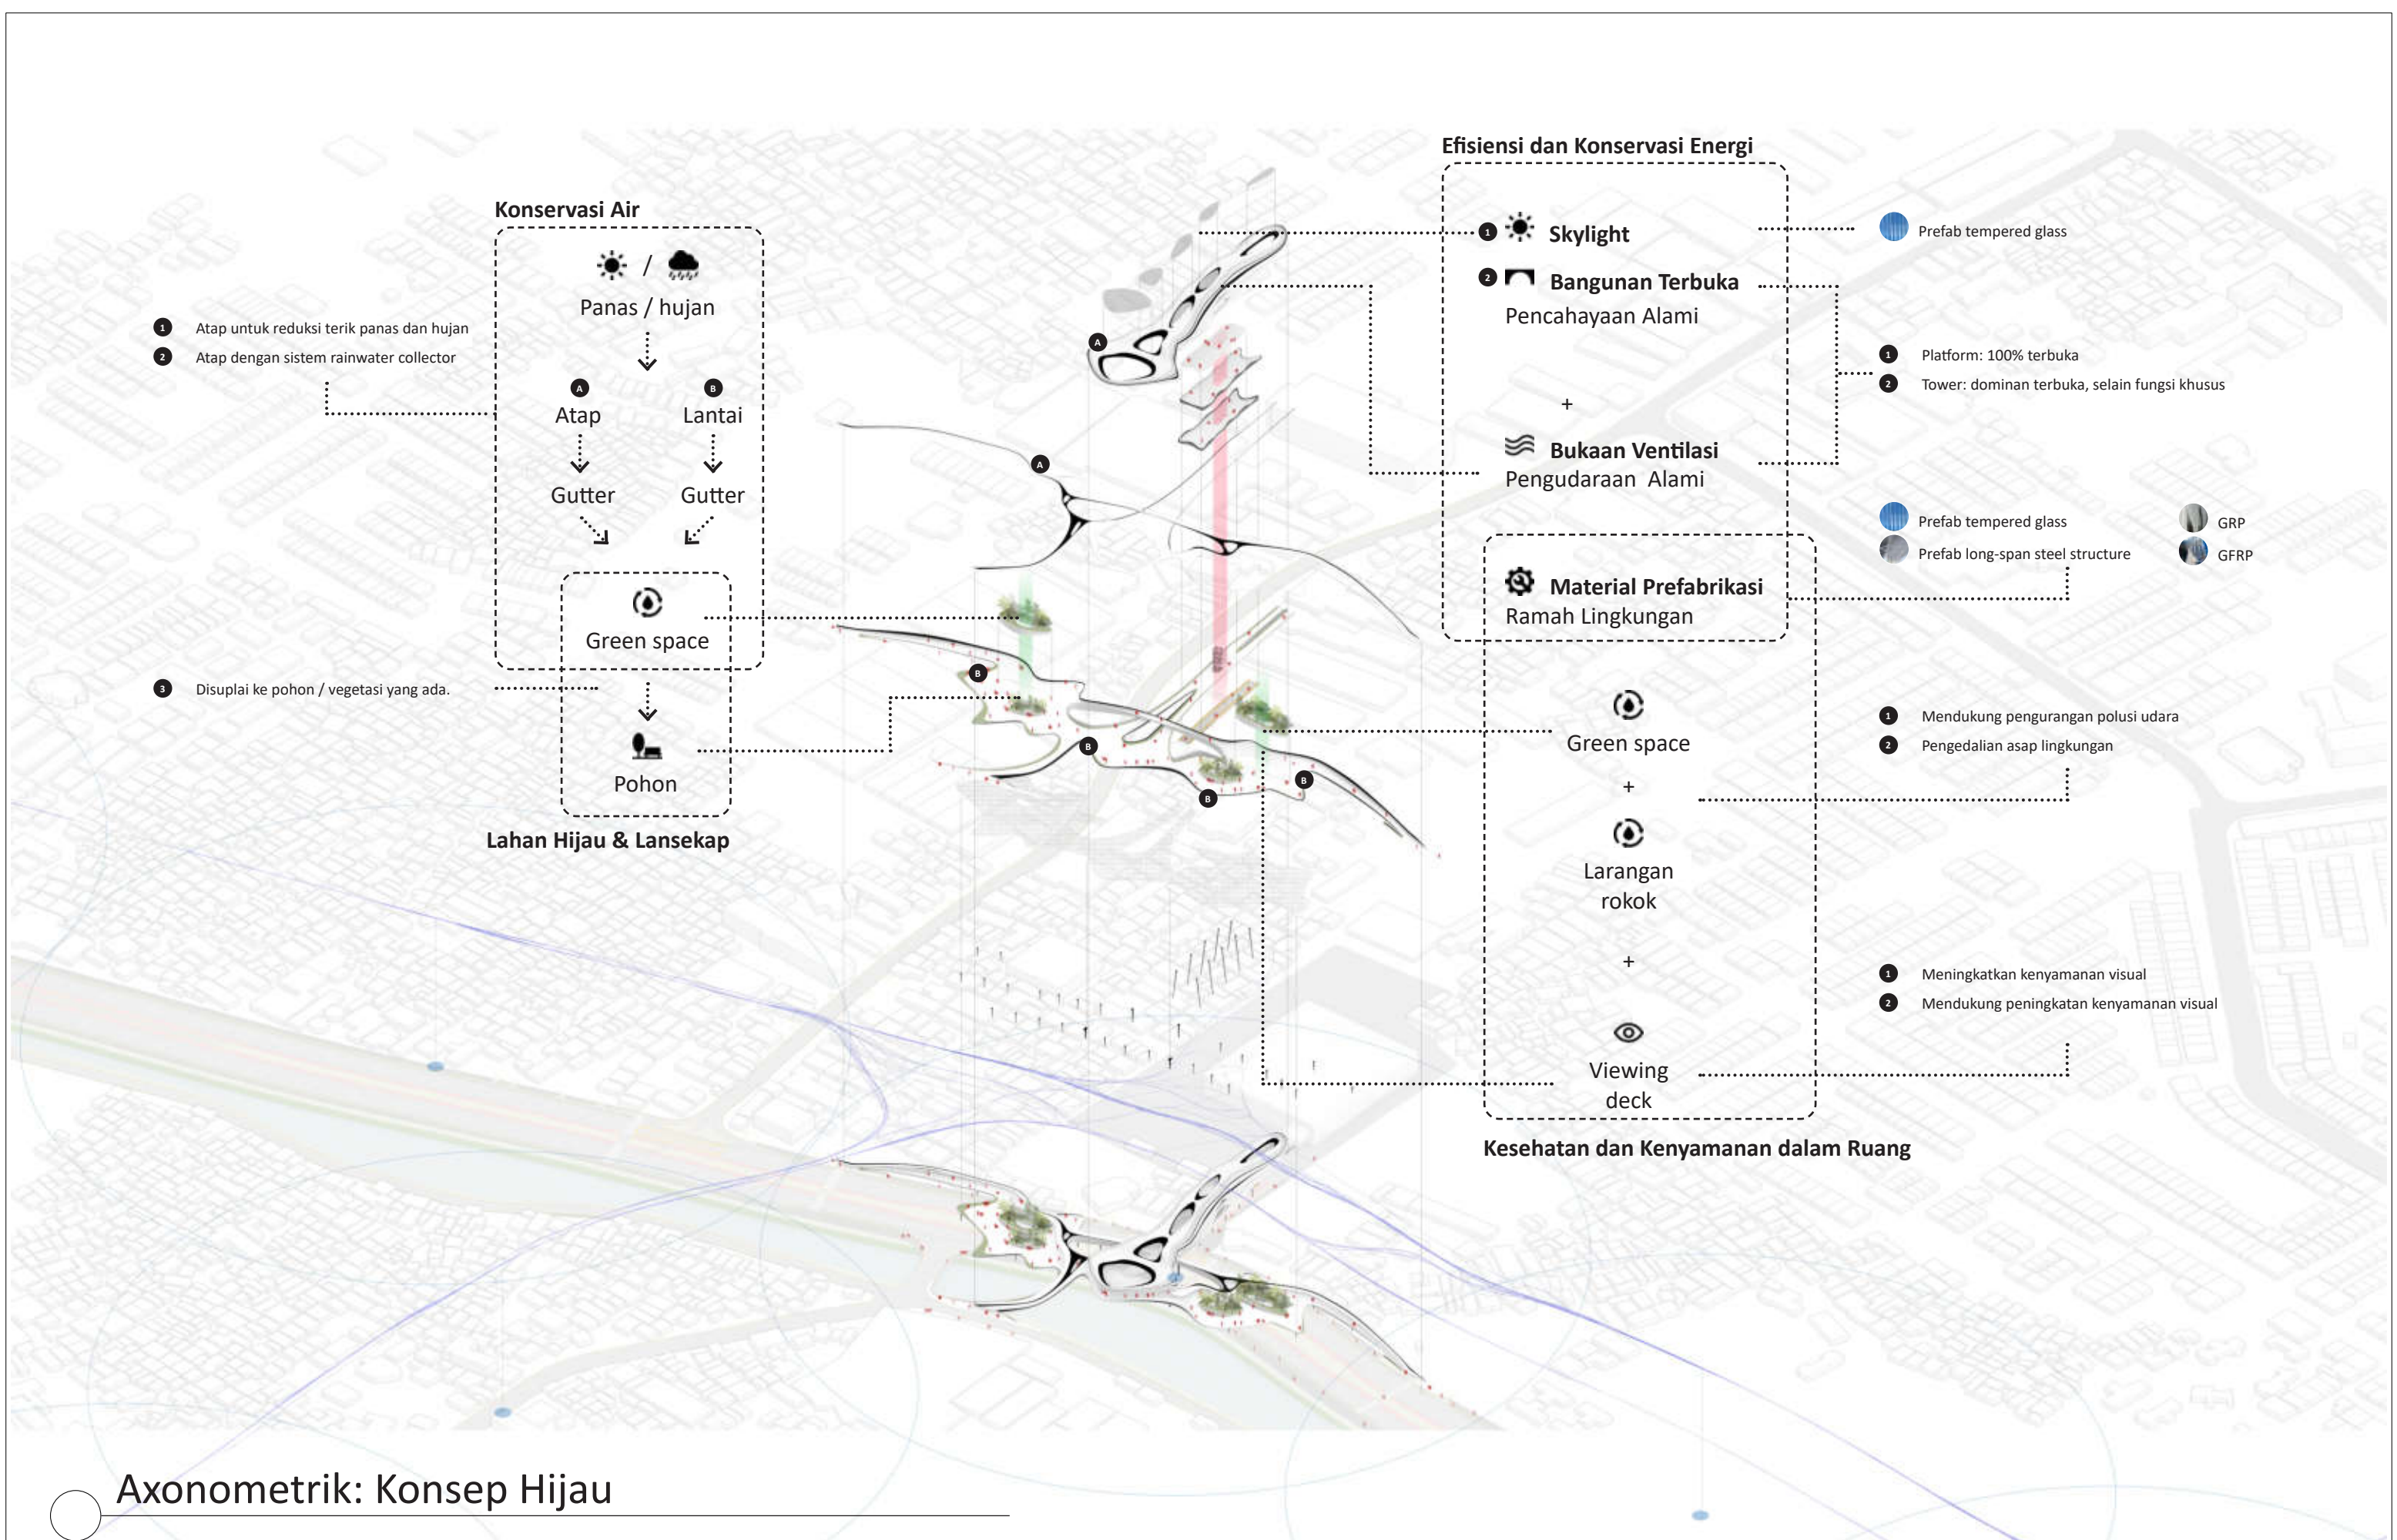


Axonometrik: Konsep Hijau

 Program Studi Magister Arsitektur Sekolah Arsitektur, Perencanaan, dan Pengembangan Kebijakan Institut Teknologi Bandung	AR6690 Tesis Semester 1 2022/2023	Kalideres Transit Hub (XTH)	Dosen Pembimbing: Aswin Indraprastha, S.T., M.T., M.Eng., Ph.D.	Nama Mahasiswa: Arnett Ferels	Tanggal: 25/01/2023
			Dosen Koordinator: Dewi Larasati, S.T, M.T, Ph.D.	NIM: 25221029	

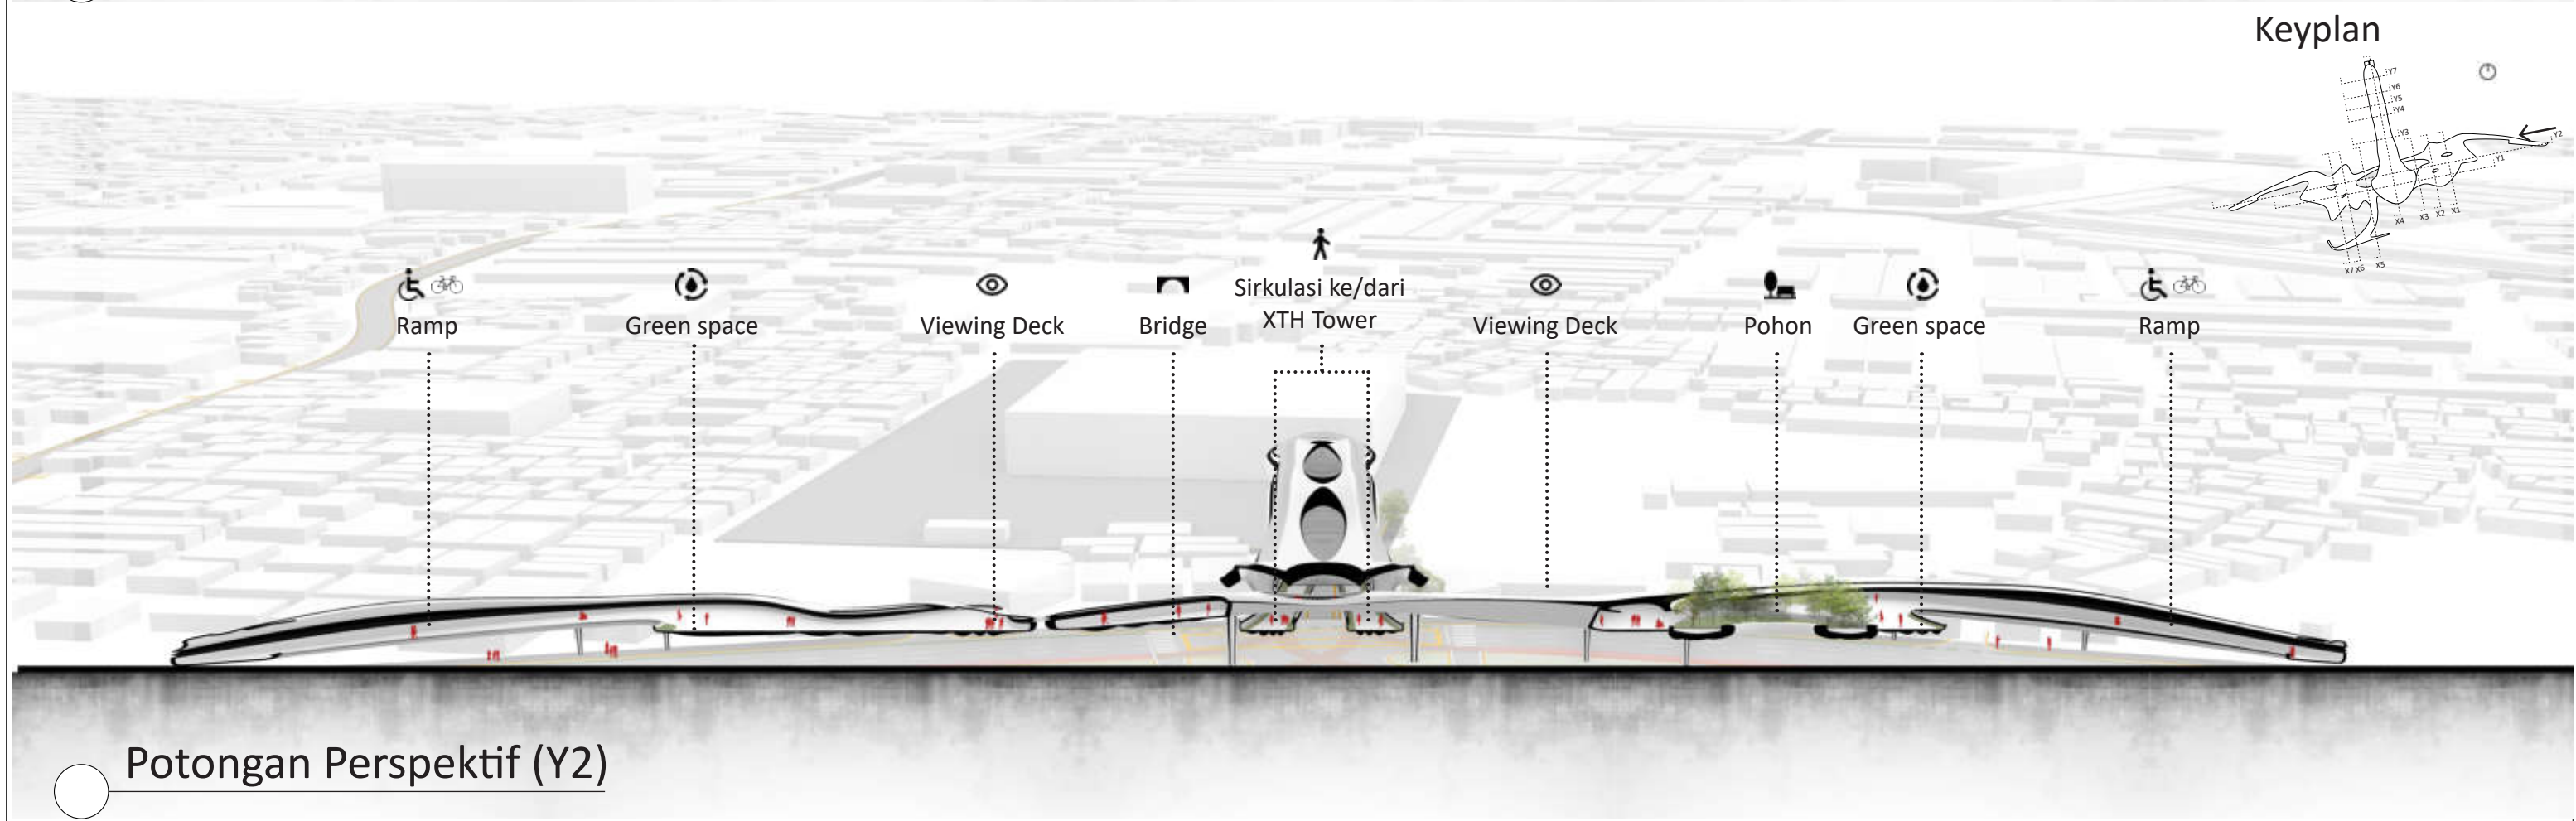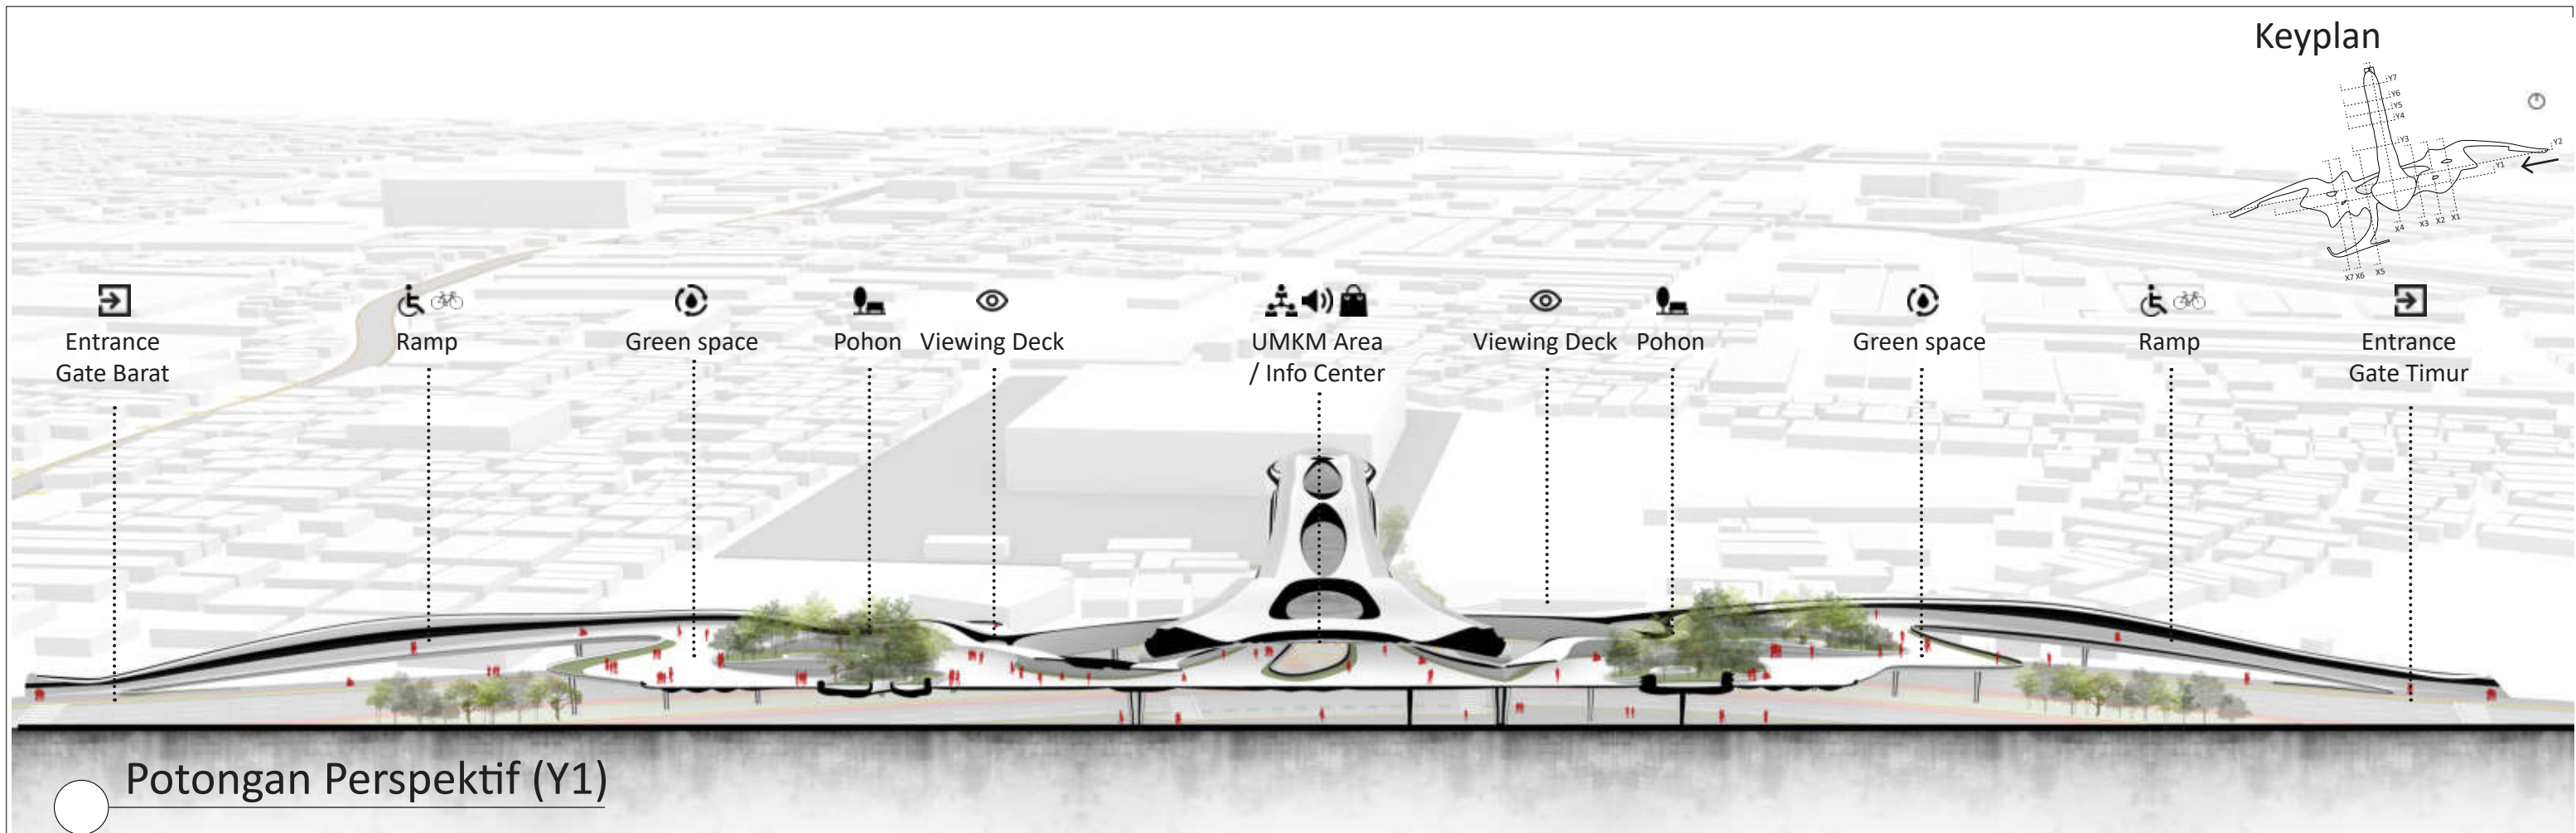


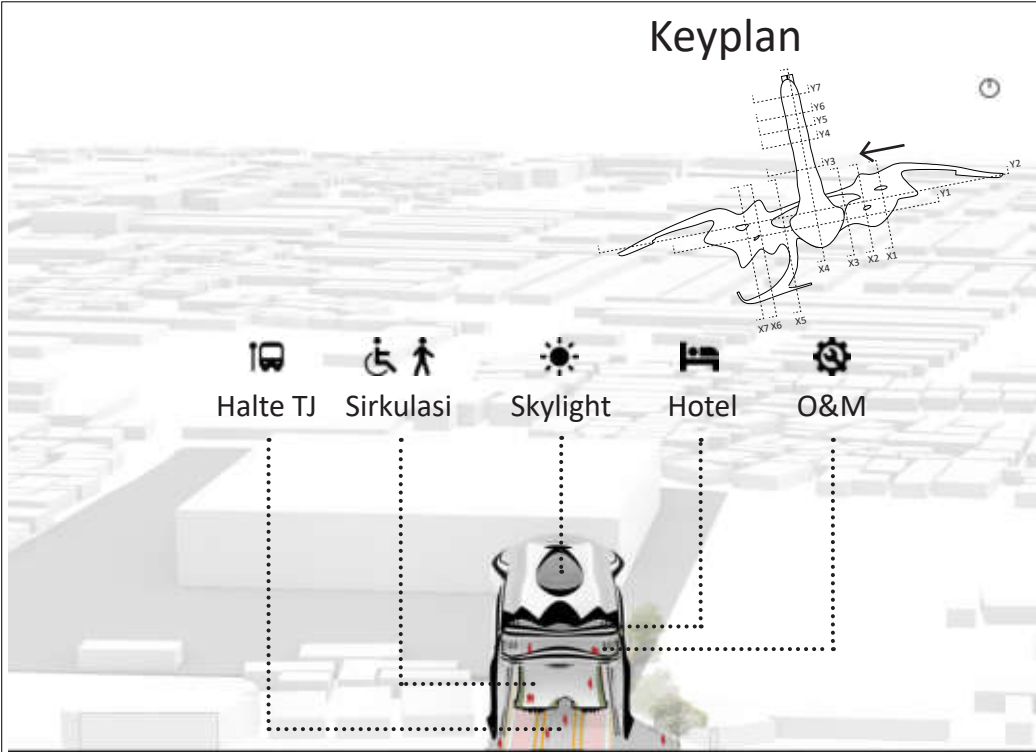


Potongan Perspektif (Y3)

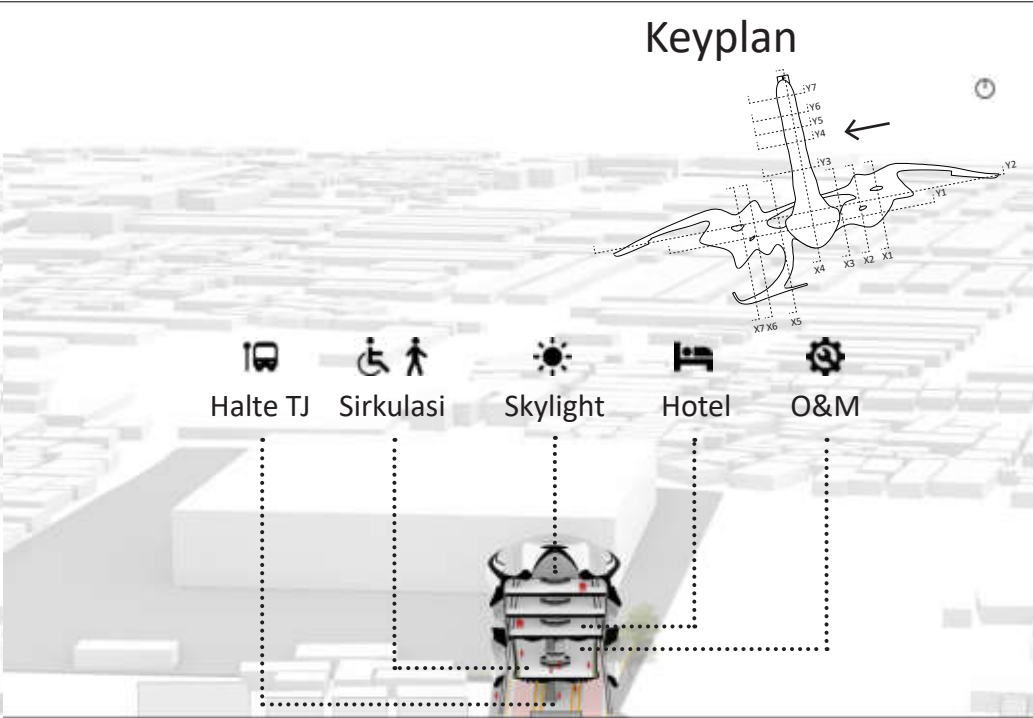


Potongan Perspektif (Y4)

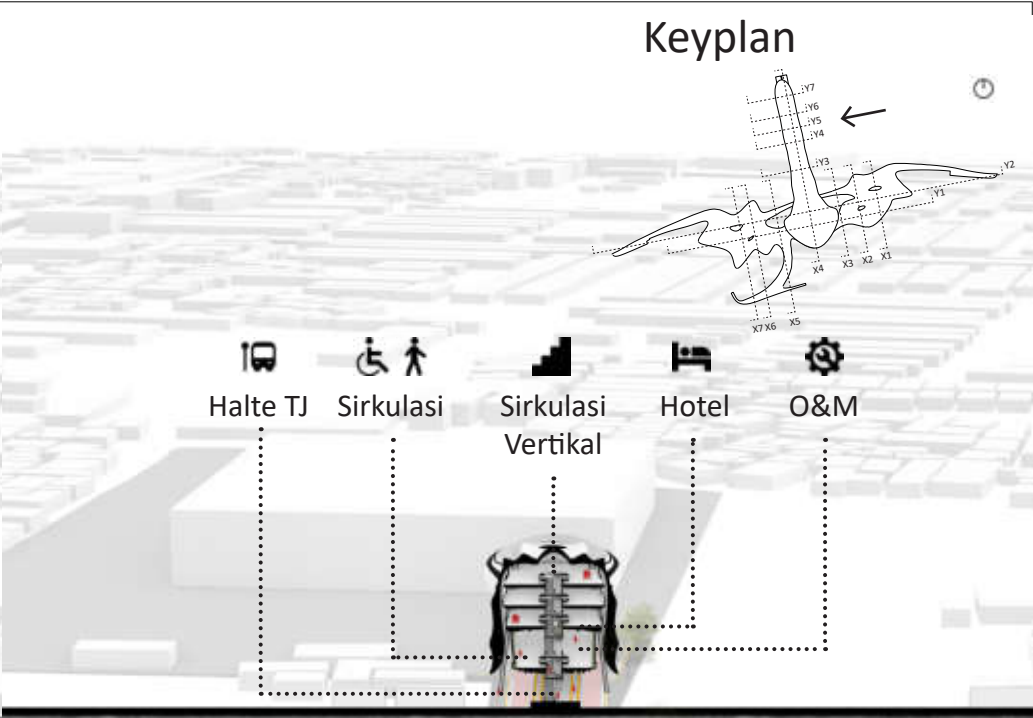

Potongan Perspektif (Y5)


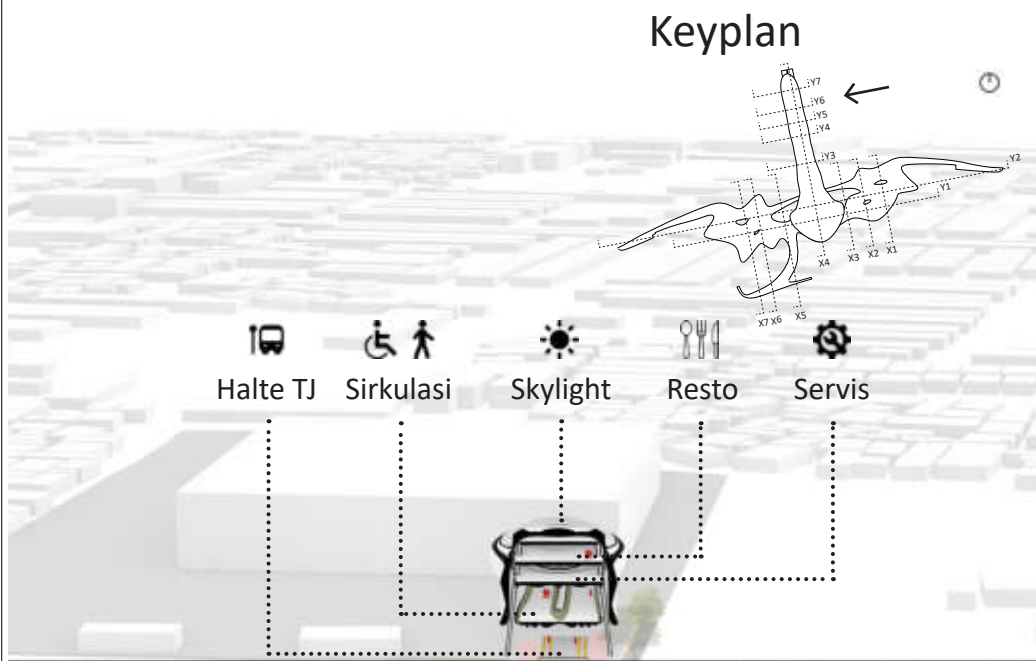


Potongan Perspektif (Y6)

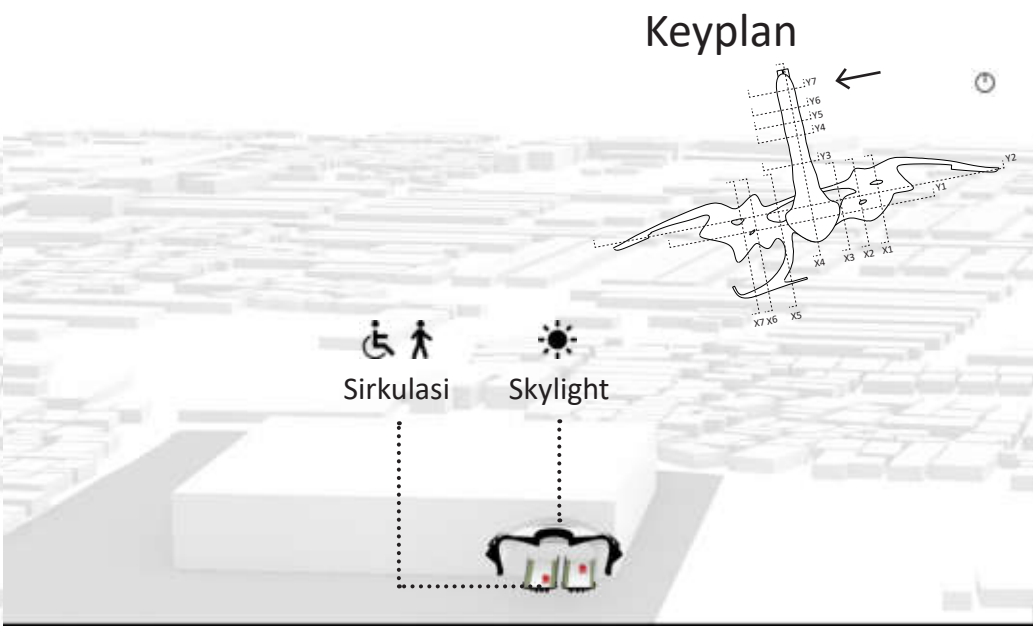


Potongan Perspektif (Y7)



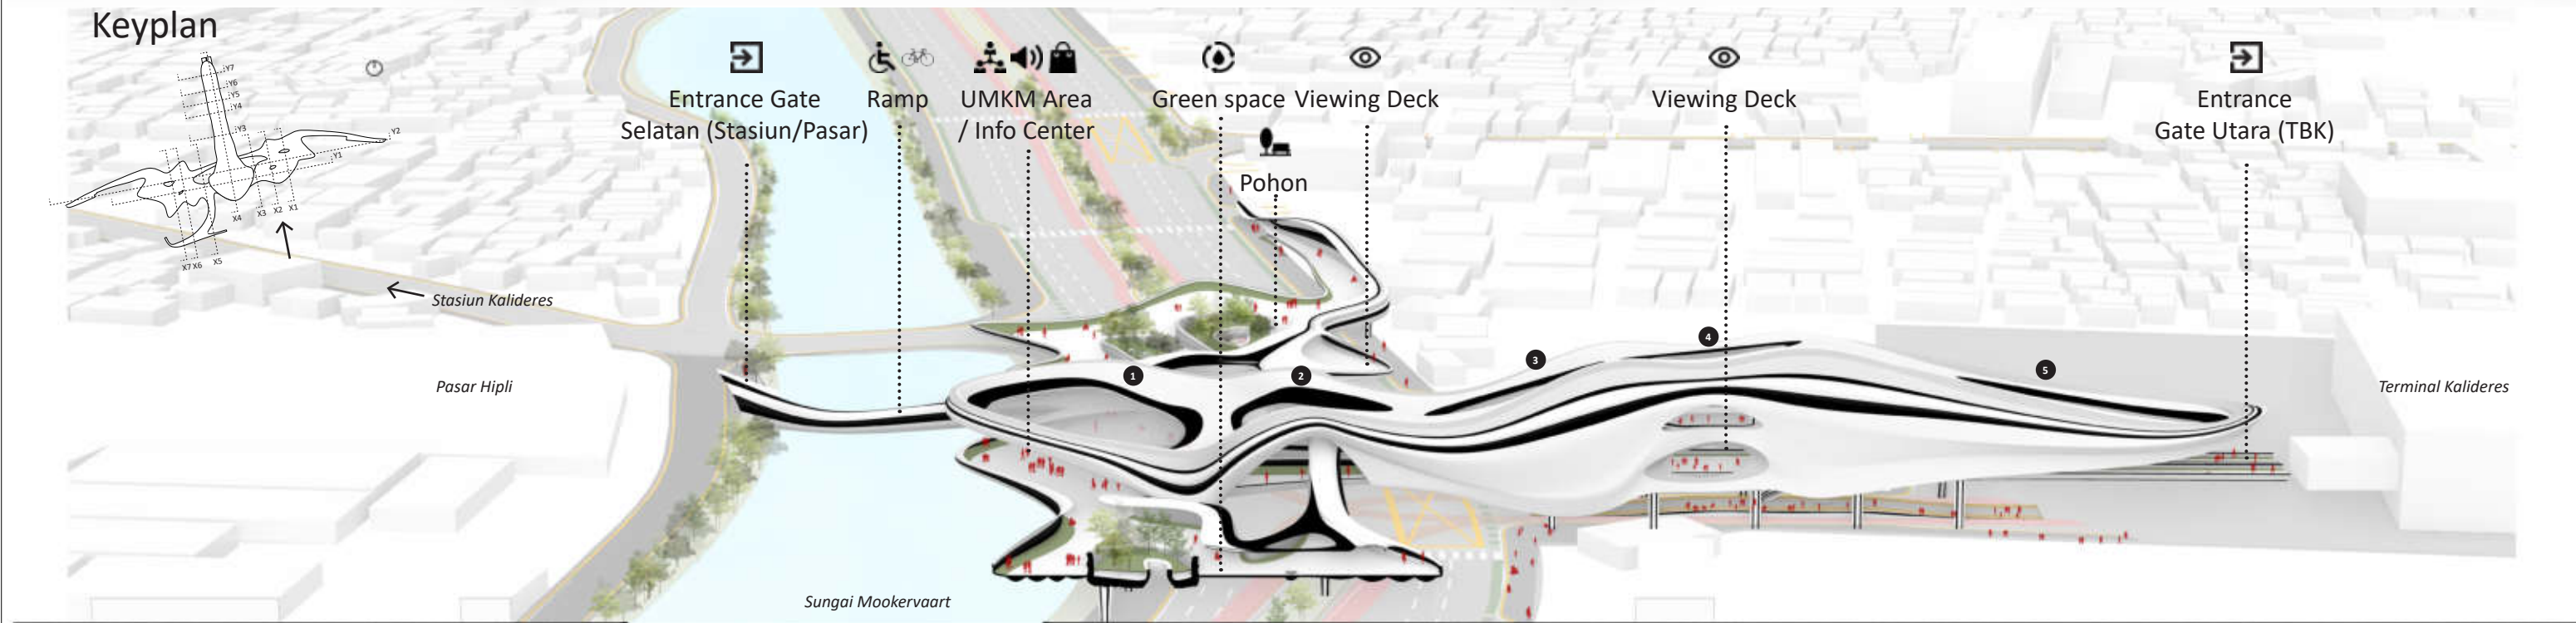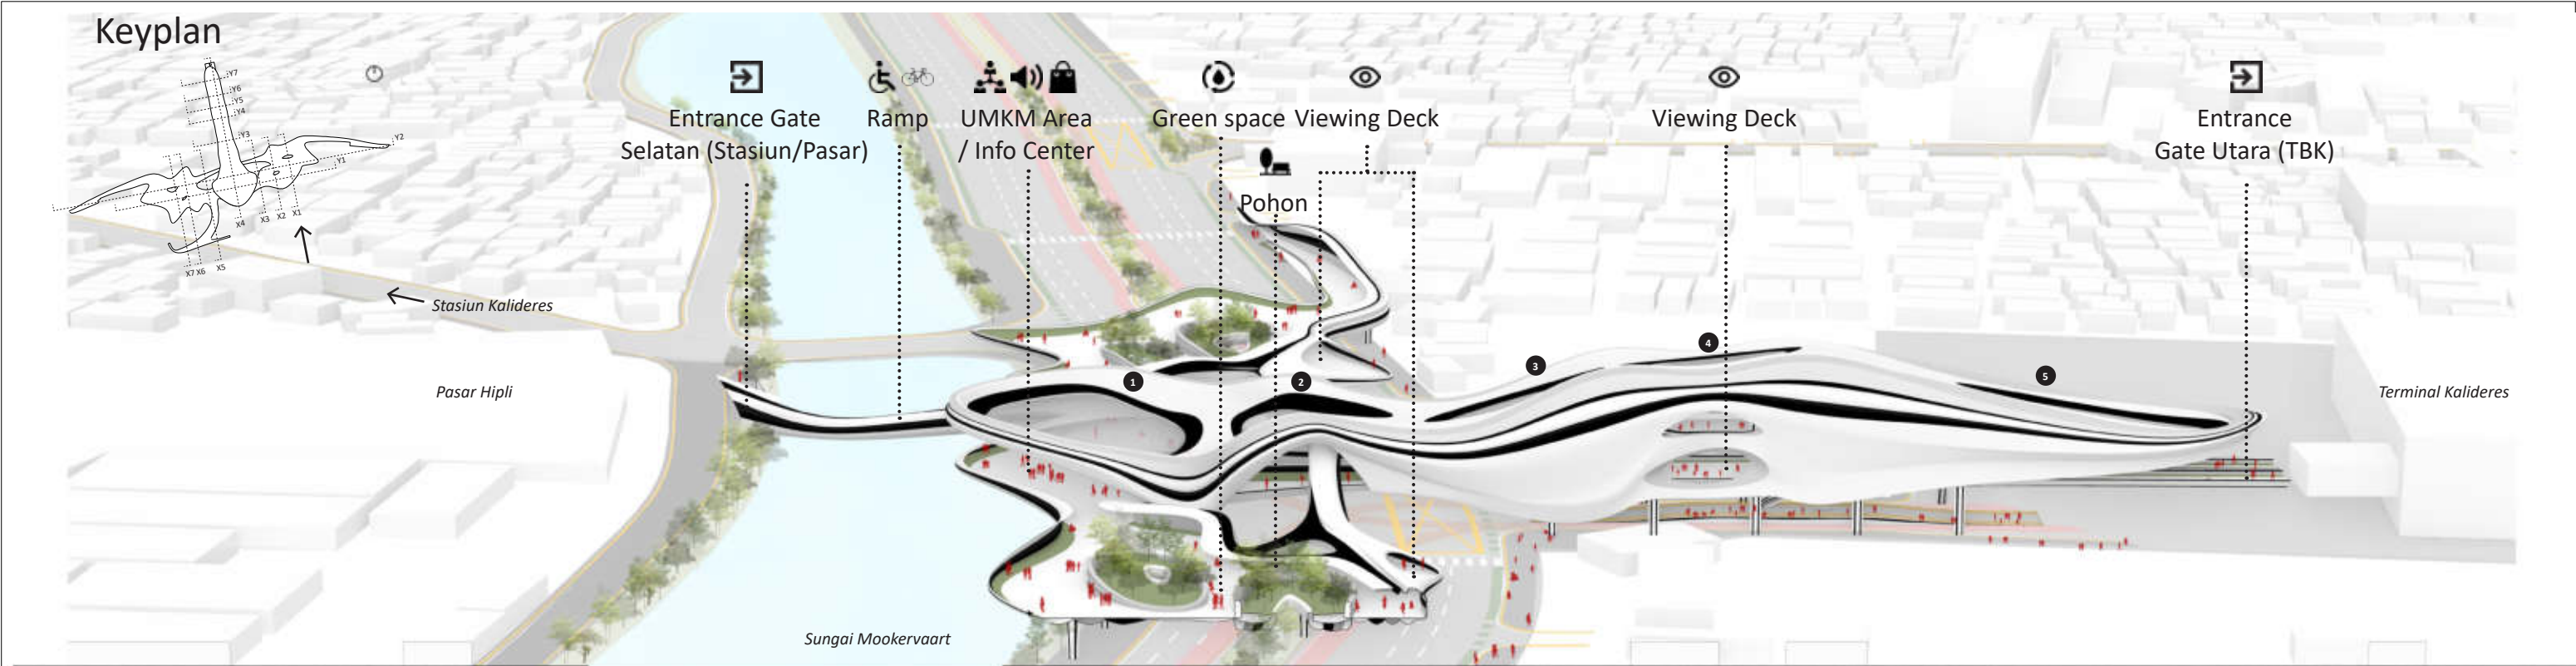


 Program Studi Magister Arsitektur Sekolah Arsitektur, Perencanaan, dan Pengembangan Kebijakan Institut Teknologi Bandung	AR6690 Tesis Semester 1 2022/2023	Kalideres Transit Hub (XTH)	Dosen Pembimbing: Aswin Indraprastha, S.T., M.T., M.Eng., Ph.D.	Nama Mahasiswa: Arnett Ferels	Tanggal: 25/01/2023
			Dosen Koordinator: Dewi Larasati, S.T, M.T, Ph.D.	NIM: 25221029	

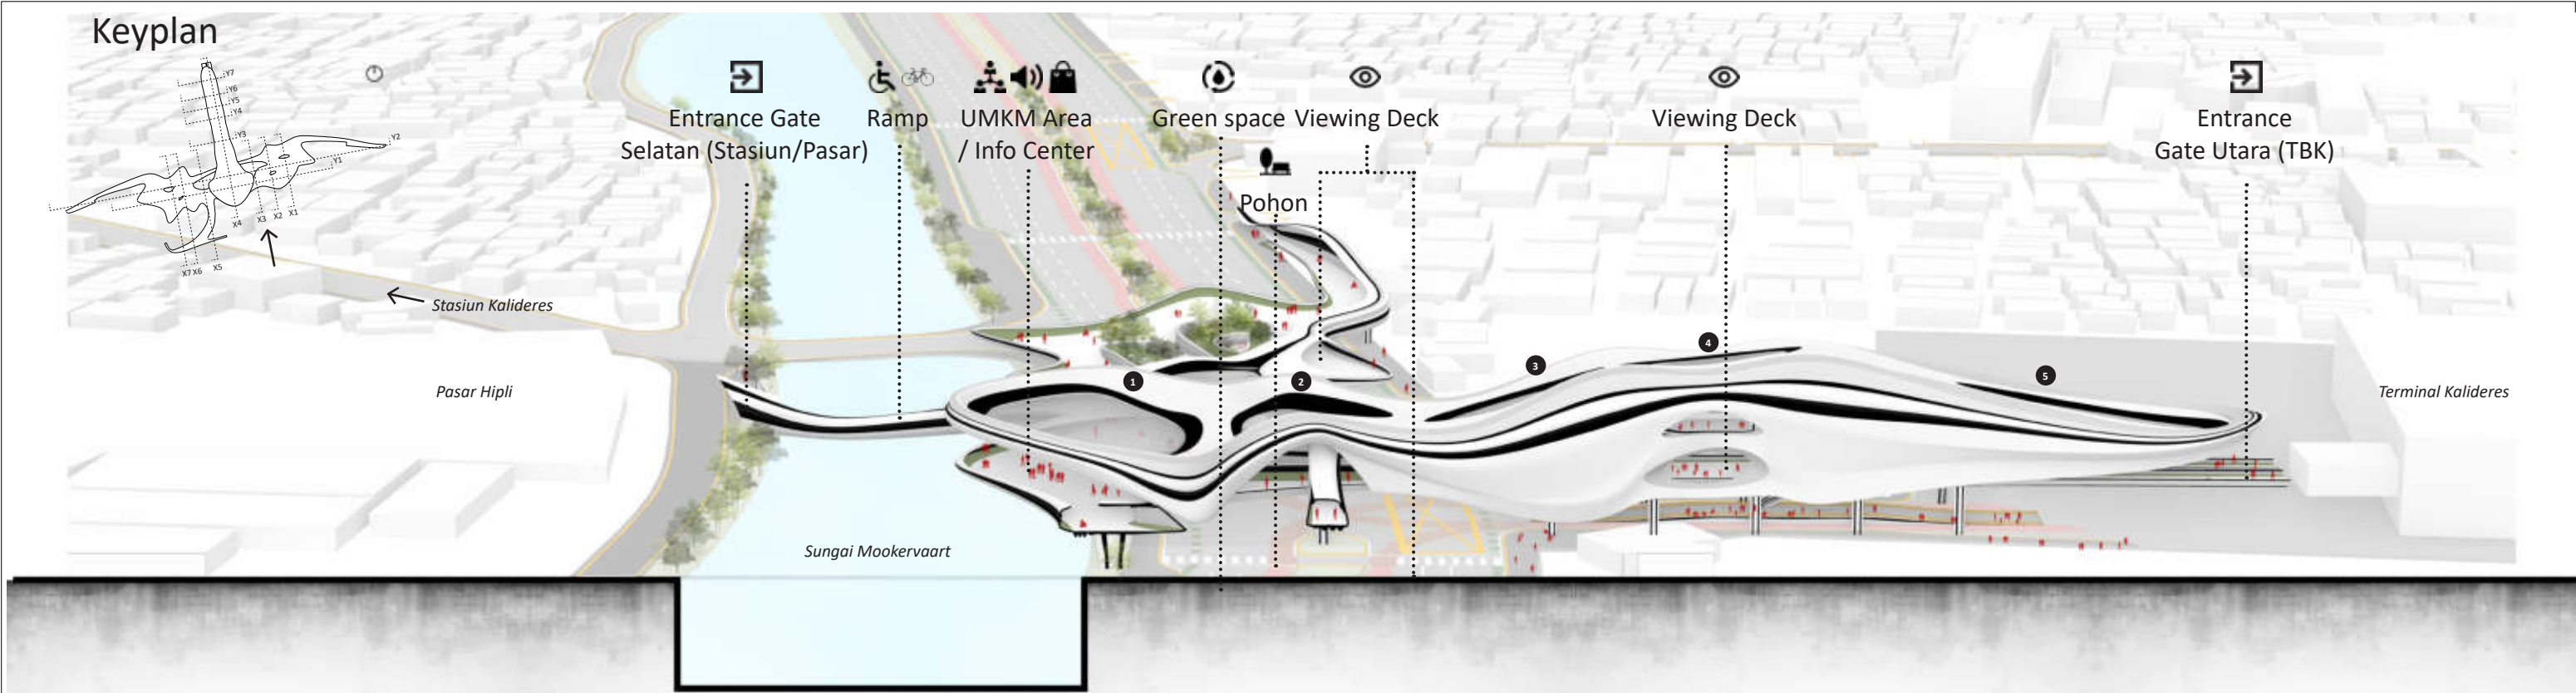

Potongan Perspektif (X3)

1 2 3 4 5 Skylight

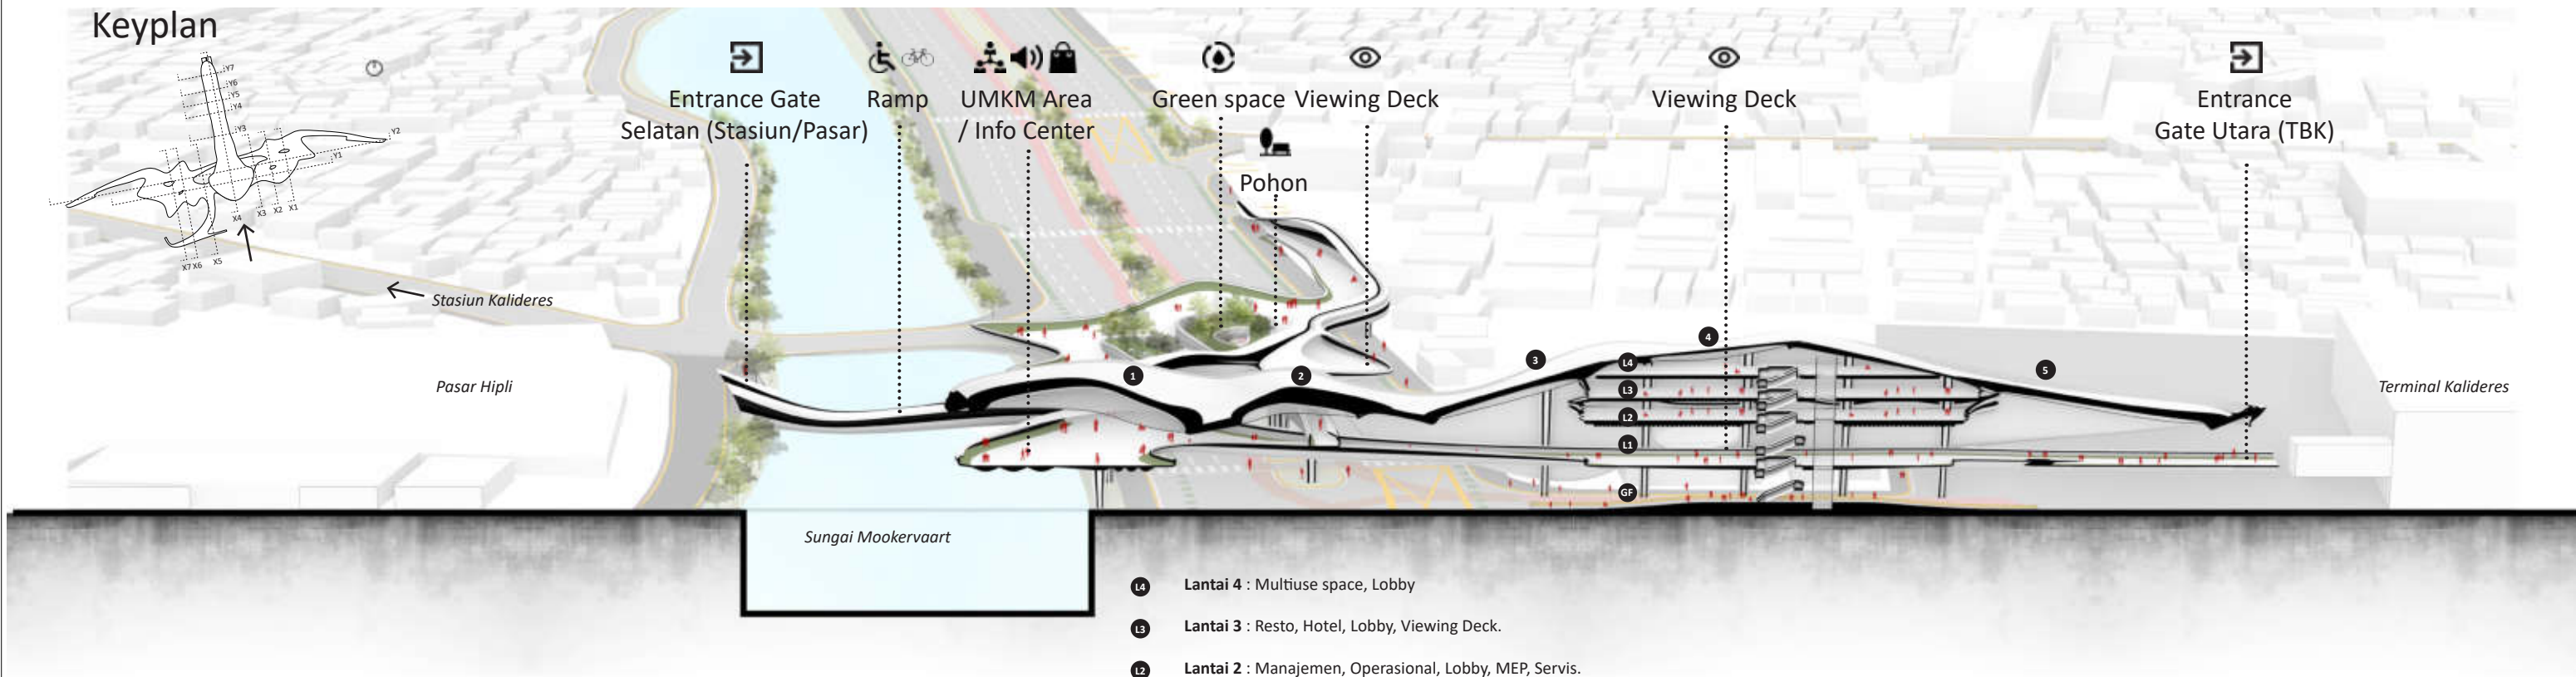


Potongan Perspektif (X4)


1 2 3 4 5 Skylight

- L4 Lantai 4 : Multiuse space, Lobby
- L3 Lantai 3 : Resto, Hotel, Lobby, Viewing Deck.
- L2 Lantai 2 : Manajemen, Operasional, Lobby, MEP, Servis.
- L1 Lantai 1 (XTH Platform): Info center, UMKM area, Viewing Deck, Green space.
- GF Lantai Dasar (GF) : Jalan raya, Halte TJ Keberangkatan dan Kedatangan.




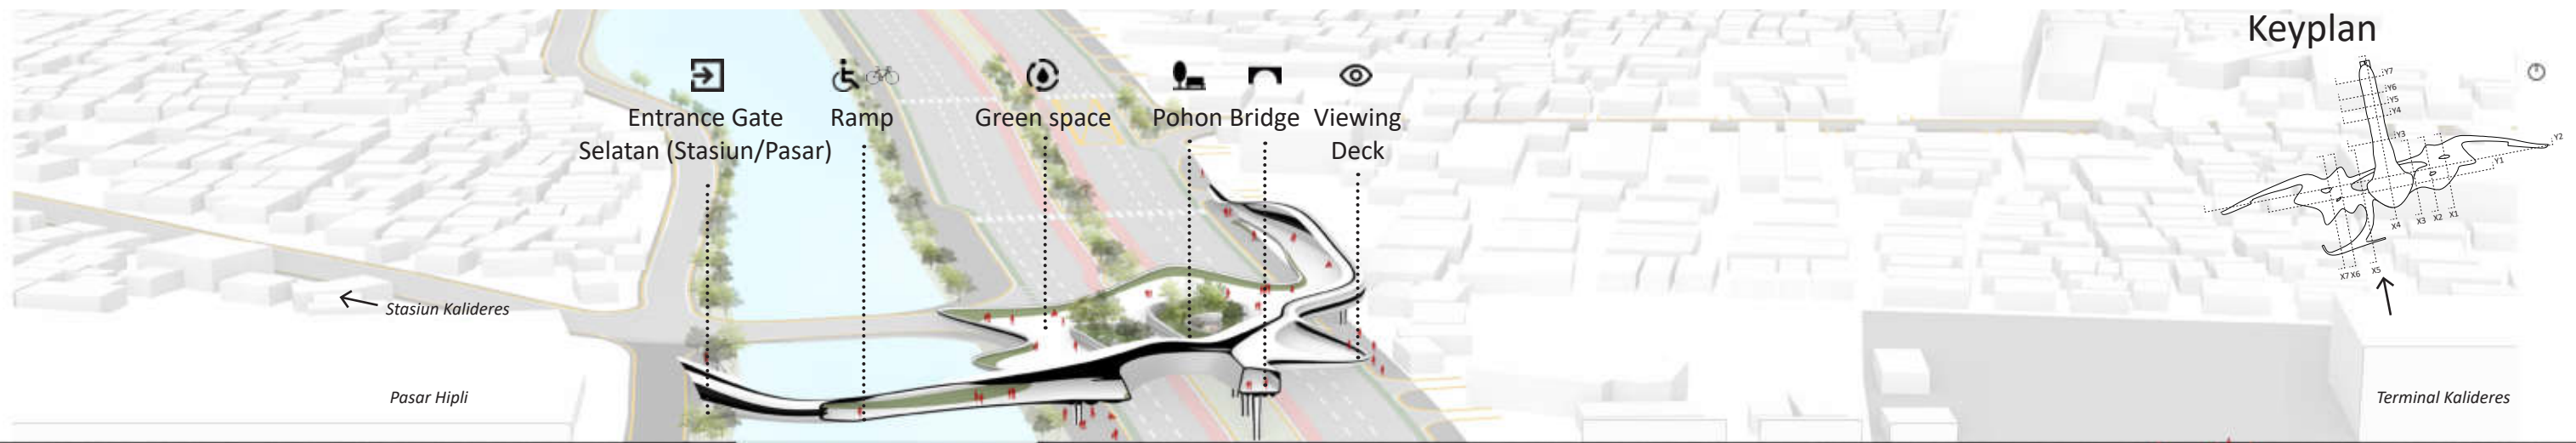

Potongan Perspektif (X5)

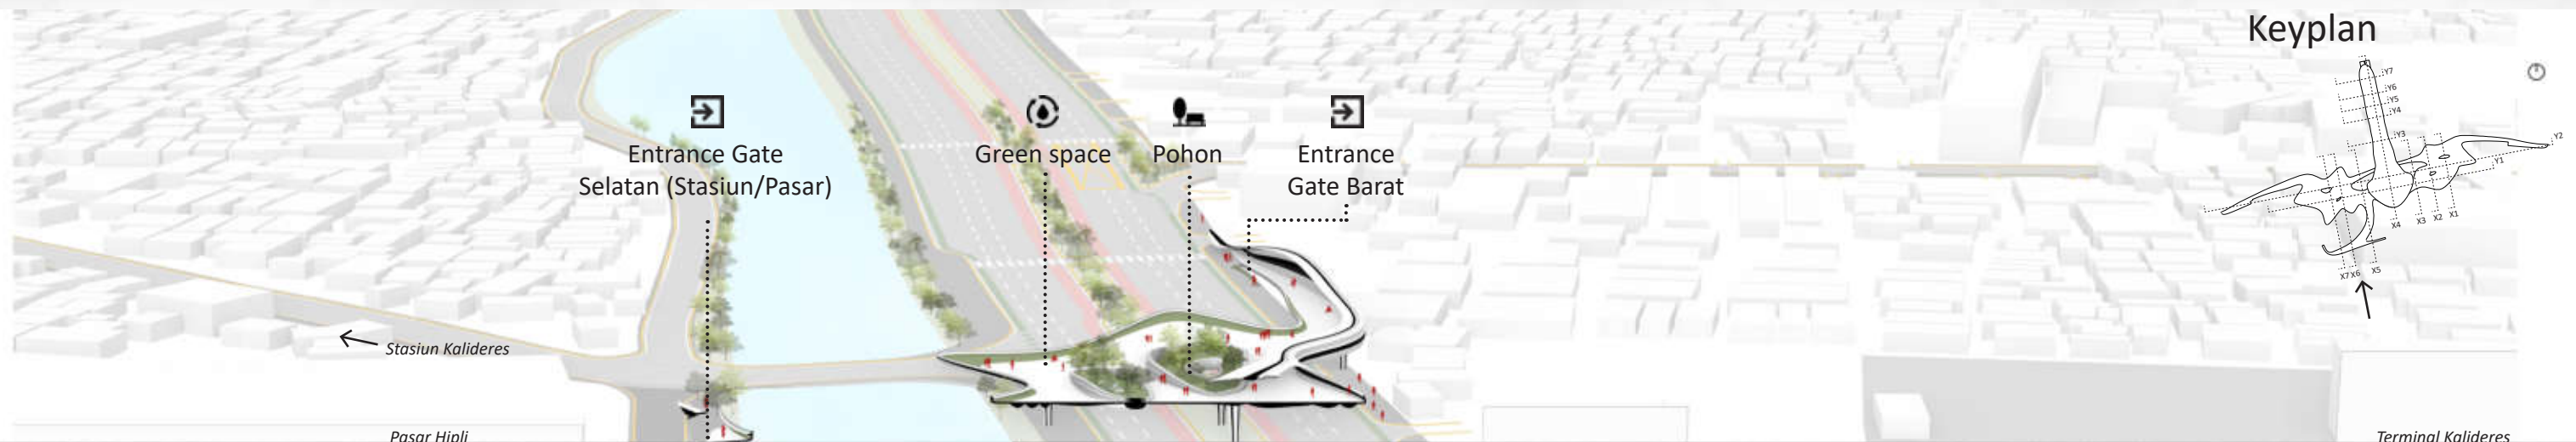

Potongan Perspektif (X6)

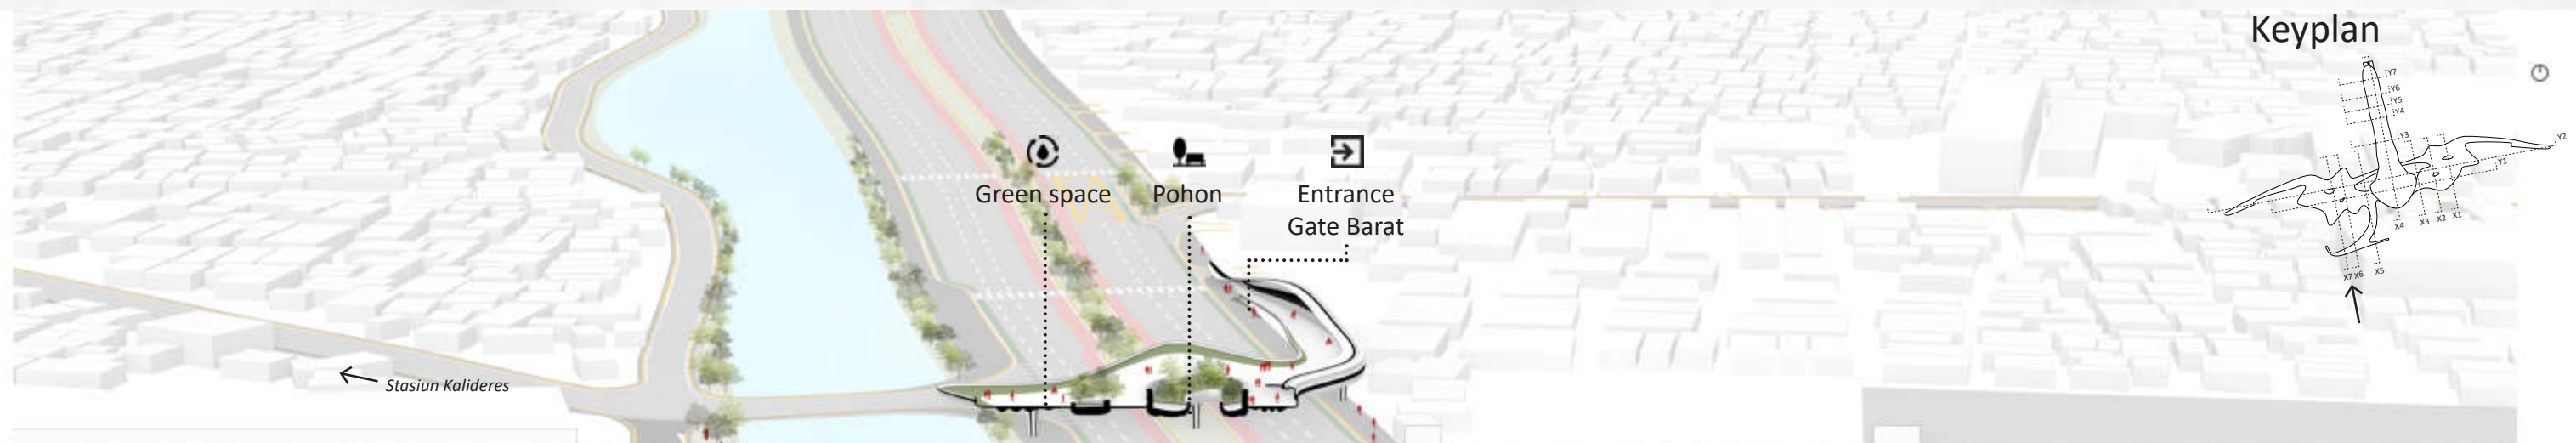


Potongan Perspektif (X7)





Bird eye

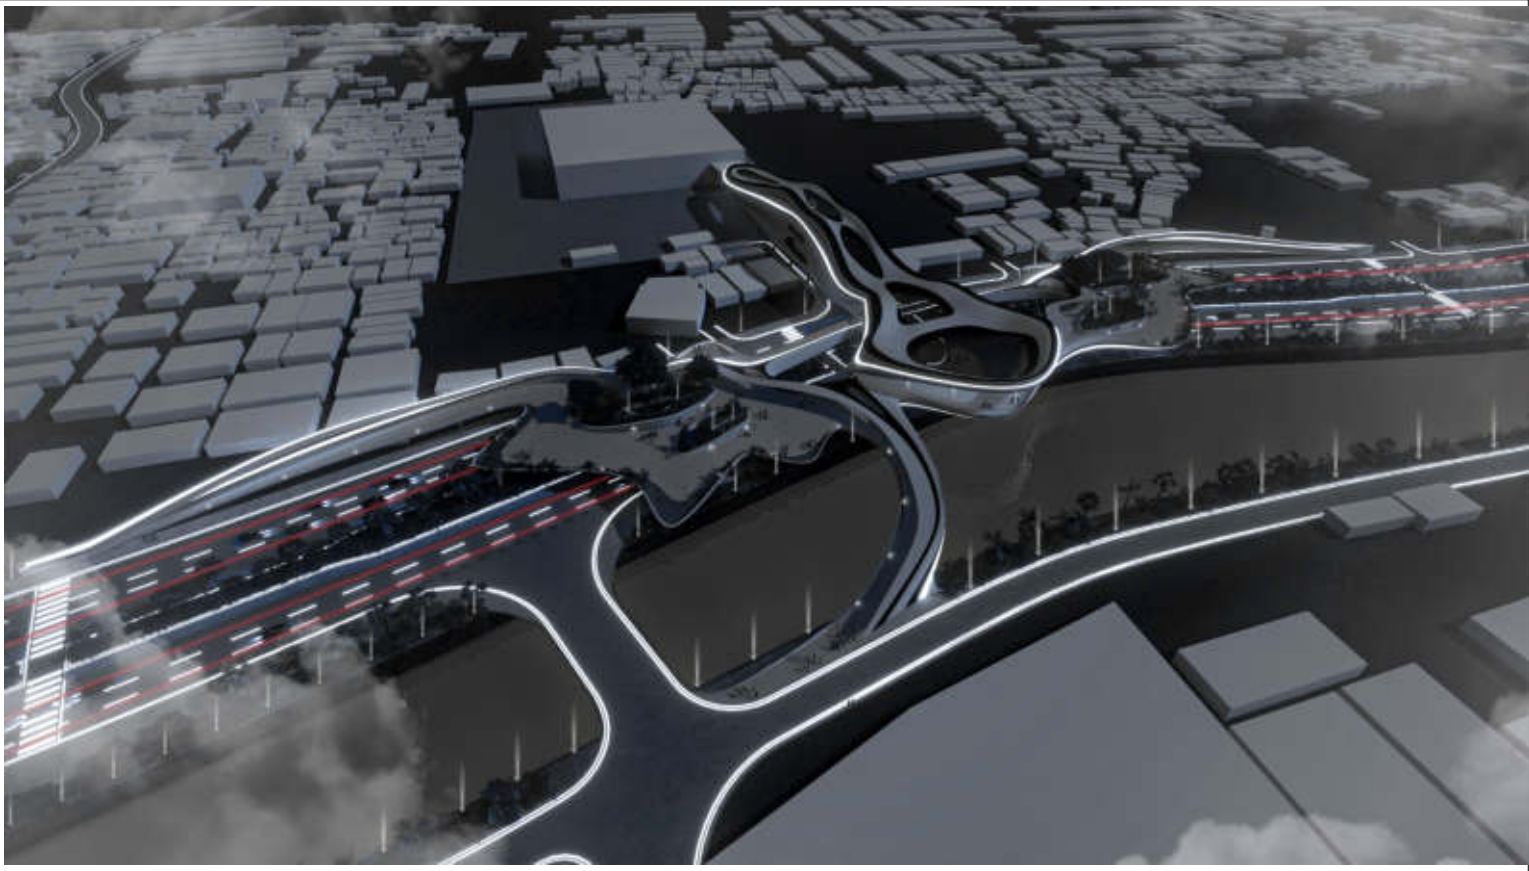

Bird eye



Platform & Central Area



Platform



Platform & Bridge

 Program Studi Magister Arsitektur Sekolah Arsitektur, Perencanaan, dan Pengembangan Kebijakan Institut Teknologi Bandung	AR6690 Tesis Semester 1 2022/2023	Kalideres Transit Hub (XTH)	Dosen Pembimbing: Aswin Indraprastha, S.T., M.T., M.Eng., Ph.D.	Nama Mahasiswa: Arnett Ferels	Tanggal: 25/01/2023
			Dosen Koordinator: Dewi Larasati, S.T, M.T, Ph.D.	NIM: 25221029	



Entrance Barat



Entrance Selatan (Stasiun/Pasar)



Entrance Timur



Green Space & Viewing Deck



Platform & Green Space



Platform & Green Space



Entrance Timur & Green Space



Platform & Viewing Deck



Viewing Deck & Tower

 Program Studi Magister Arsitektur Sekolah Arsitektur, Perencanaan, dan Pengembangan Kebijakan Institut Teknologi Bandung	AR6690 Tesis Semester 1 2022/2023	Kalideres Transit Hub (XTH)	Dosen Pembimbing: Aswin Indraprastha, S.T., M.T., M.Eng., Ph.D. Dosen Koordinator: Dewi Larasati, S.T, M.T, Ph.D.	Nama Mahasiswa: Arnett Ferels NIM: 25221029	Tanggal: 25/01/2023
--	--	------------------------------------	---	---	--------------------------------



Tower & Atrium



Central Area: UMKM & Info Center



Central Area: UMKM & Info Center



Tower (dari arah TBK)



Jalan Raya & Void



Jalan Raya & Void



Tower & Atrium



Bridge



Platform & Bridge

 Program Studi Magister Arsitektur Sekolah Arsitektur, Perencanaan, dan Pengembangan Kebijakan Institut Teknologi Bandung	AR6690 Tesis Semester 1 2022/2023	Kalideres Transit Hub (XTH)	Dosen Pembimbing: Aswin Indraprastha, S.T., M.T., M.Eng., Ph.D.	Nama Mahasiswa: Arnott Ferels	Tanggal: 25/01/2023
			Dosen Koordinator: Dewi Larasati, S.T, M.T, Ph.D.	NIM: 25221029	



Halte TJ Keberangkatan



Halte TJ Kedatangan



Halte TJ



Lantai 3 (Resto, Hotel)



Lantai 4 (Multiuse space)



Lantai 4 (Multiuse space)



Tower & Ceiling Pattern


 Program Studi Magister Arsitektur Sekolah Arsitektur, Perencanaan, dan Pengembangan Kebijakan Institut Teknologi Bandung	AR6690 Tesis Semester 1 2022/2023	Kalideres Transit Hub (XTH)	Dosen Pembimbing: Aswin Indraprastha, S.T., M.T., M.Eng., Ph.D. Dosen Koordinator: Dewi Larasati, S.T, M.T, Ph.D.	Nama Mahasiswa: Arnett Ferels NIM: 25221029	Tanggal: 25/01/2023
--	--	------------------------------------	---	---	--------------------------------



Jalan Raya & Void



Platform

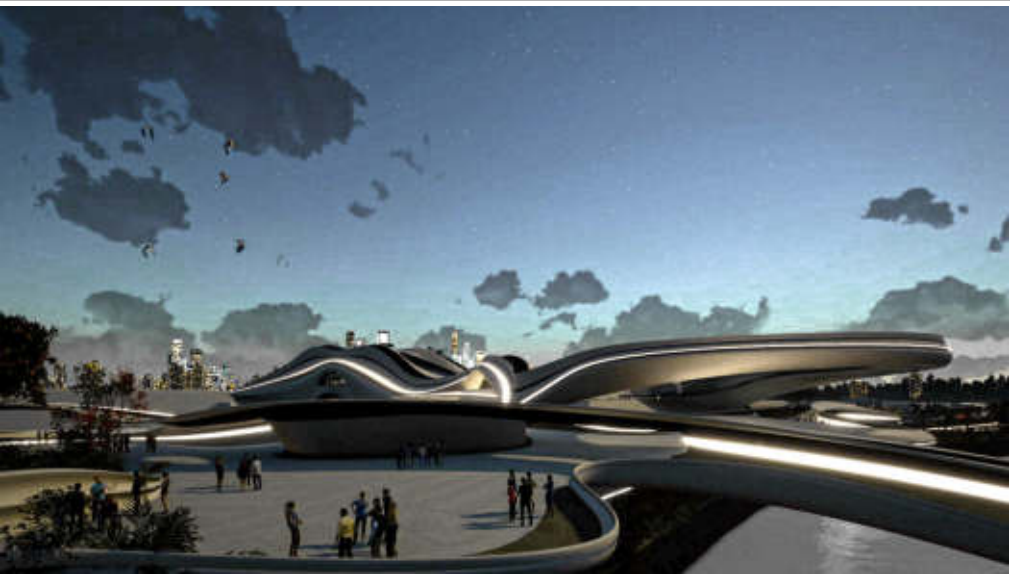

Platform & Green Space



Green Space & Viewing Deck



Platform



Platform & Green Space



Halte TJ



Tower & Ceiling Pattern



Central Area: UMKM & Info Center

 Program Studi Magister Arsitektur Sekolah Arsitektur, Perencanaan, dan Pengembangan Kebijakan Institut Teknologi Bandung	AR6690 Tesis Semester 1 2022/2023	Kalideres Transit Hub (XTH)	Dosen Pembimbing: Aswin Indraprastha, S.T., M.T., M.Eng., Ph.D. Dosen Koordinator: Dewi Larasati, S.T, M.T, Ph.D.	Nama Mahasiswa: Arnett Ferels NIM: 25221029	Tanggal: 25/01/2023
--	--	------------------------------------	---	---	--------------------------------